BELEGBLATT

SGD-Nr. / Titel: 8768 — RA 01 02 03 — N3,SONDIERUNGEN FUER SBB-UNTERFUEHRUNG N FELDMOOS, E LACHEN

Selektion: 1.36LAA 2. 3. 4. — Mut. 3

	11	12	13	14	15	16	17	18	19	20	
Anzahl Records (RA)											
Geologie	120 67 122	120 61 120									
Km-Netz	708 227	708 227									
Kartenblatt	1133	1133									
Verfügbarkeit	-0										

Verfalldatum:

Datum Autor(en): 2403970 Autor(en) JAE — Mut. 3

Auftraggeber: Strasseninspektorat des Kantons Schwyz, Abt. Nationalstrassen

Dokument-zusammensetzung


Bericht	Notiz	Anzahl Seiten	Graphika, als Beilage oder allein	Tafeln, Abbildungen	Tabelle	Diagramme	Fotografien	Situation 1:1000	geol.Bohrprofile 1:50 Tiefen: 6,00m	Rammprofile 1:50 Tiefen: 6,00m
	1	1	9					1	8	8

Originalkennzeichen des Dokumentes: 70.058 (Brief v.1.4.70)

Geograph.Lage: (Koordinaten) (oder Gebiet)* Schwerpunkt ca. 708'18/227'75

Standort: SGD

EB

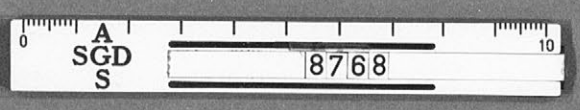

Zürich, den 1. April 197o
K/rh

Herrn
A. Marty
Ingenieurbüro
8853 L a c h e n / SZ

Betrifft: Nationalstrasse N 3
Unterführung der SBB in Lachen

Sehr geehrter Herr Marty,

In der Beilage übermitteln wir Ihnen von den Piezometerrohren, welche für die Beobachtung der Grundwasserabsenkung bei der SBB-Unterführung der N 3 in Lachen durch uns abgeteuft wurden, die Sondierprotokolle und einen dazugehörigen Situationsplan im Doppel.

Mit freundlichen Grüssen

Beilage erwähnt

A
SGD
S
8768

Gnossenländer

Zipfel & Co.

NEUE BRÜCKE ÜBER DEN SPREITENBACH

von Lachen

Kostengrenze

Nationalstrasse N3

Fa Baas GmbH

Genossame Lachen

BAULINIE

ÜBERFÜHRUNG SBB

Rv = 2000 m
tv = 71.90 m
t = 1.29 m

Rv = 4800 m
tv = 152.90 m
fv = 2.435 m

Rv = 265 m
tv = 10.00 m
fv = 0.19 m

3.62%
514.22 m

2.76%
420 m

7.52%
96.50 m

22.22 m

1. 2. 3. 4. 5. 7. 8.

R = 1494.12

a = 409.890 L = 112.45 m

Situation 1:1000

A
SGD
S
8768

Strasseninspektorat
des Kantons Schwyz

24. März 1970

Piezometerrohre für Beobachtung


der Grundwasserabsenkung bei der

SBB-Unterführung der N3 in Lachen

Situation 1:1000

70717

Dr. Heinrich Jäckli
Geologe Zürich-Höngg
Limmattal-Strasse 289

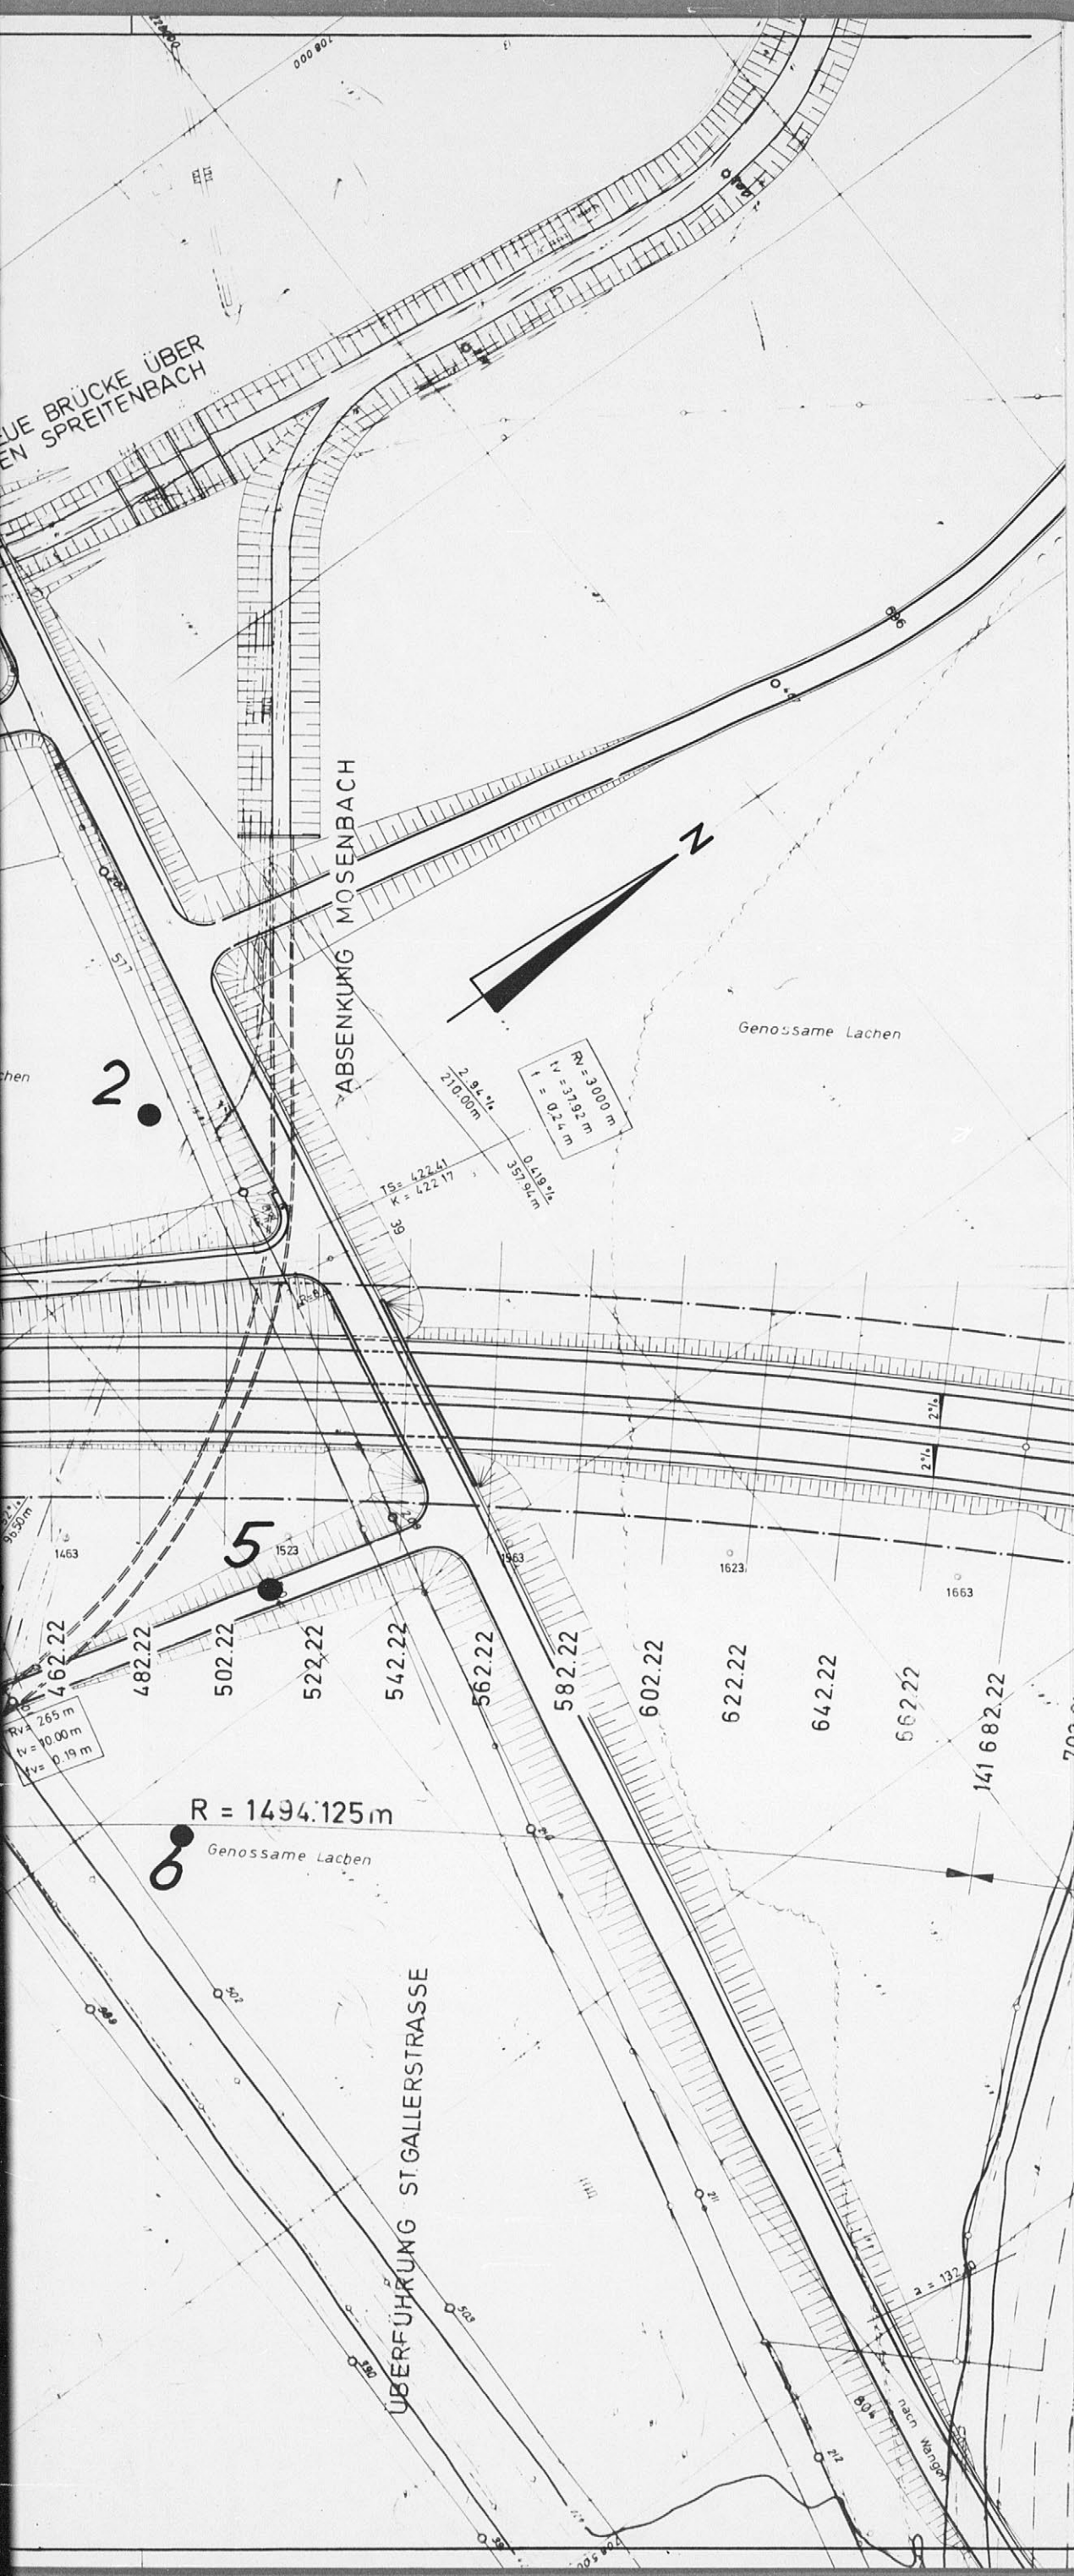


Plangrundlagen
Situation = Grundbuchvermessung
Nachgeführt bis Dez. 66

Höhenkurven = photogr. Auswertung
aus Flugaufnahmen vom 12 4 62
Neuer Horizont, R.P.N. = 373,6 m ü.M.

J. SCHENKEL
Techn. Bureau für
VERMESSUNG
8008 ZÜRICH

23

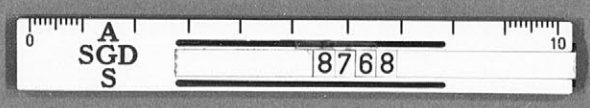

Dr. Heinrich Jäckli
Geologe
Zürich-Höngg
Limmattal-Strasse 289


Nationalstrasse N 3

Unterführung der SBB in Lachen

Piezometerrohre für die Beobachtung der Grundwasserabsenkung

24. März 197o


R.

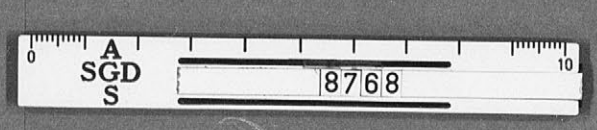

Baugrundsondierung No. 1

Objekt N 3, SBB Unterführung Lachen
Beobachtungsrohre für Grundwasserabsenkung


Datum: 29.1.197o

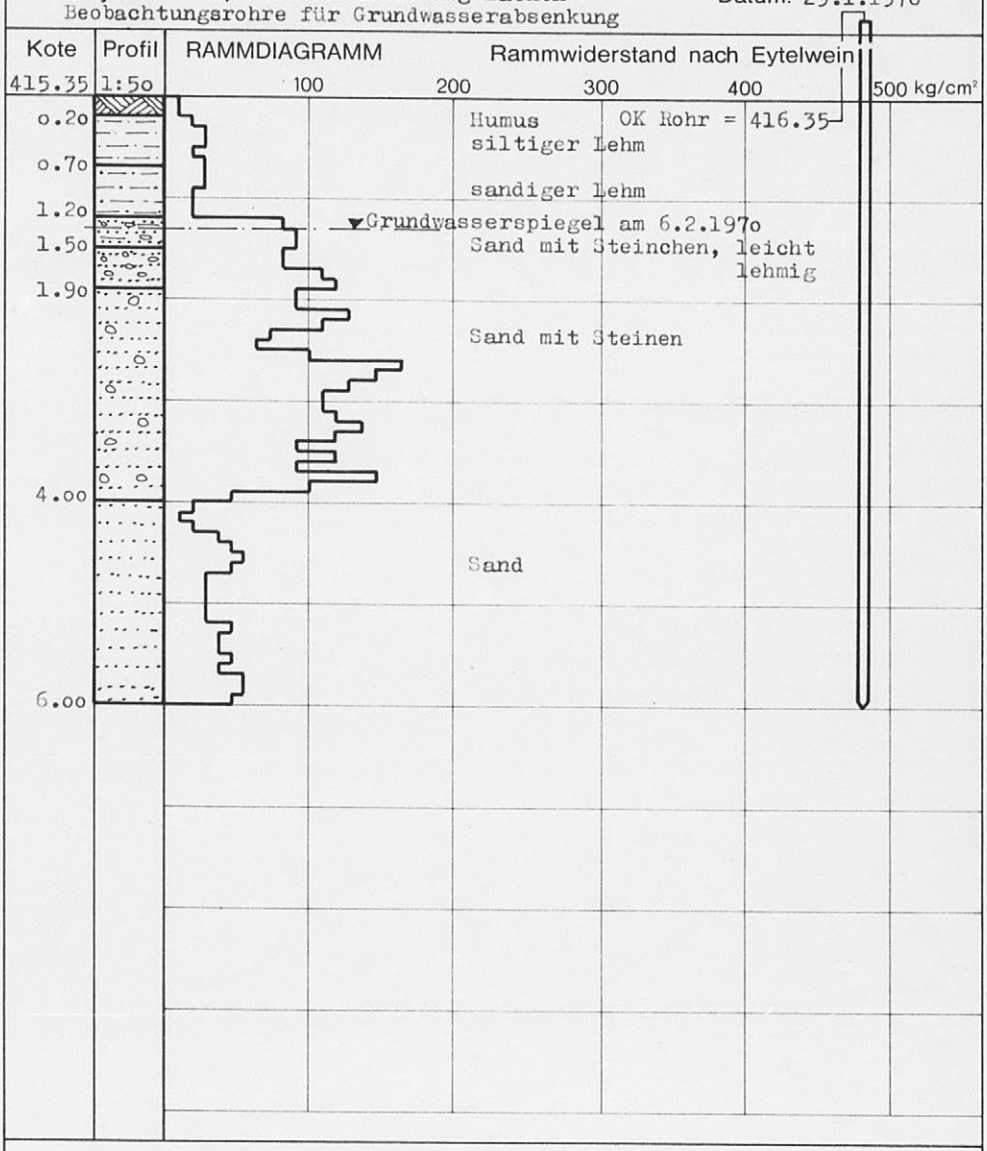

Rammgewicht: 45 kg
Fallhöhe: 20 cm
Spitzenquerschnitt: 10 cm²
Wasserstand: 2.35 m ab OK Rohr

7o717


Dr. Heinrich Jäckli
Geologe Zürich – Höngg
Limmattal-Strasse 289

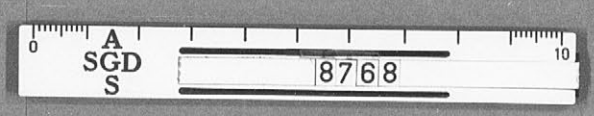

Baugrundsondierung No. 2

Objekt N 3, SBB Unterführung Lachen
Beobachtungsrohre für Grundwasserabsenkung


Datum: 4.2.197o

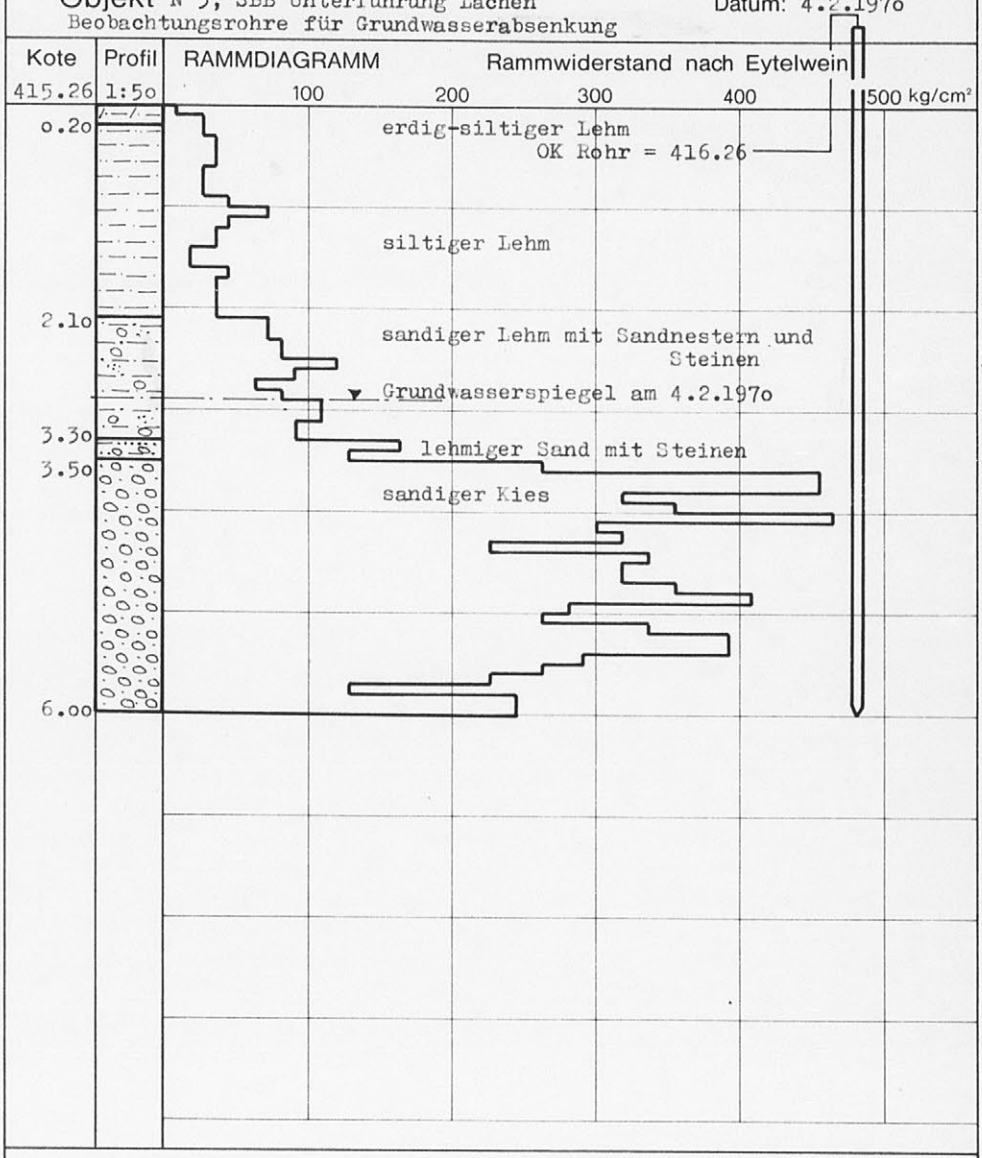

Rammgewicht:	45 kg
Fallhöhe:	20 cm
Spitzenquerschnitt:	10 cm²
Wasserstand:	3.9o m u. OK Rohr

Dr. Heinrich Jäckli
Geologe Zürich – Höngg
Limmattal-Strasse 289


7o717

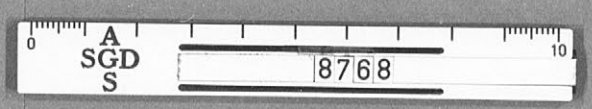

Baugrundsondierung No. 3

Objekt N 3, SBB Unterführung Lachen
Beobachtungsrohre für Grundwasserabsenkung


Datum: 5.2.197o

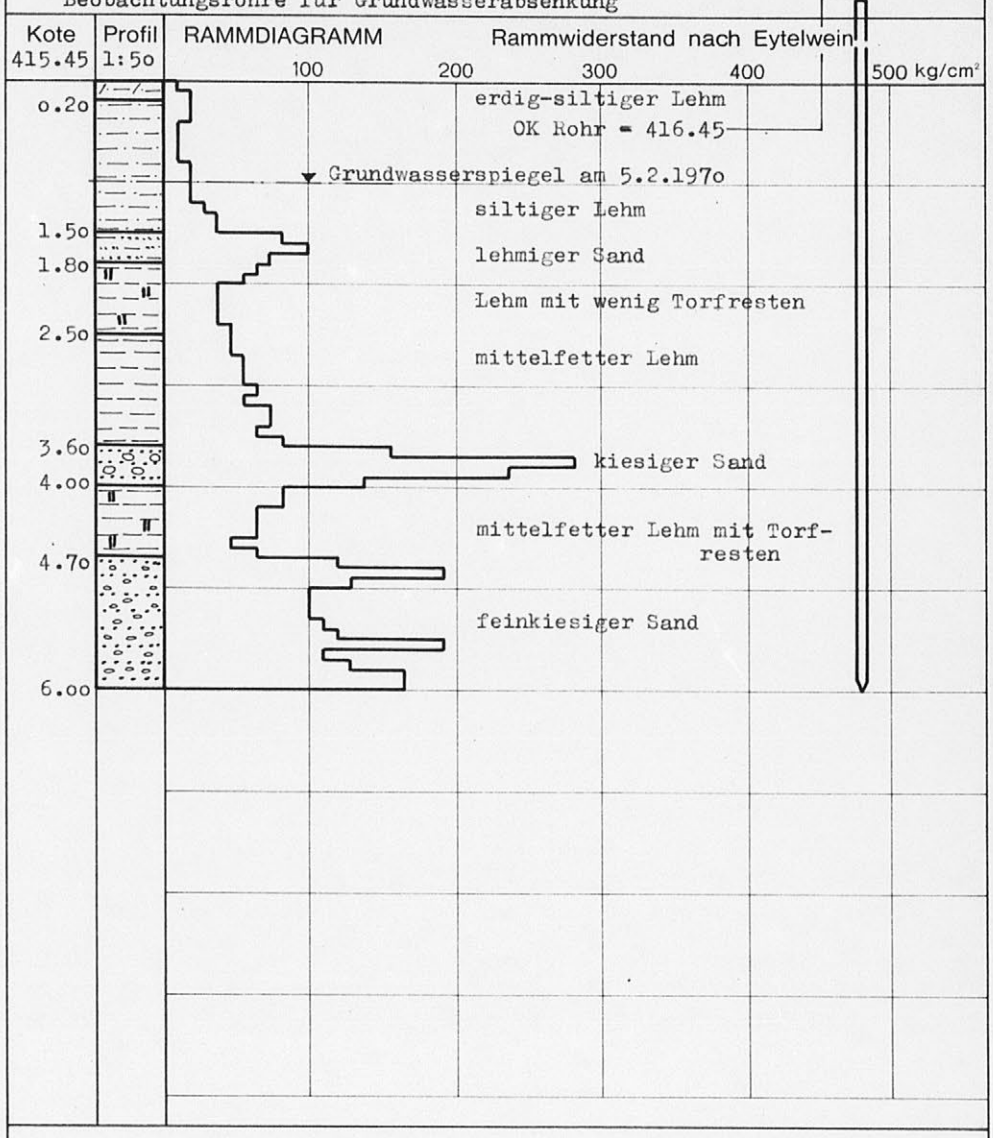

Rammgewicht:	45 kg
Fallhöhe:	20 cm
Spitzenquerschnitt:	10 cm²
Wasserstand:	2.oo m u.OK Rohr

Dr. Heinrich Jäckli
Geologe Zürich – Höngg
Limmattal-Strasse 289


7o717

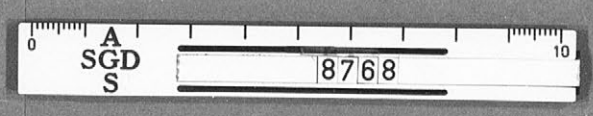

Baugrundsondierung No. 4

Objekt N 3, SBB Unterführung Lachen
Beobachtungsrohre für Grundwasserabsenkung


Datum: 6.2.197o

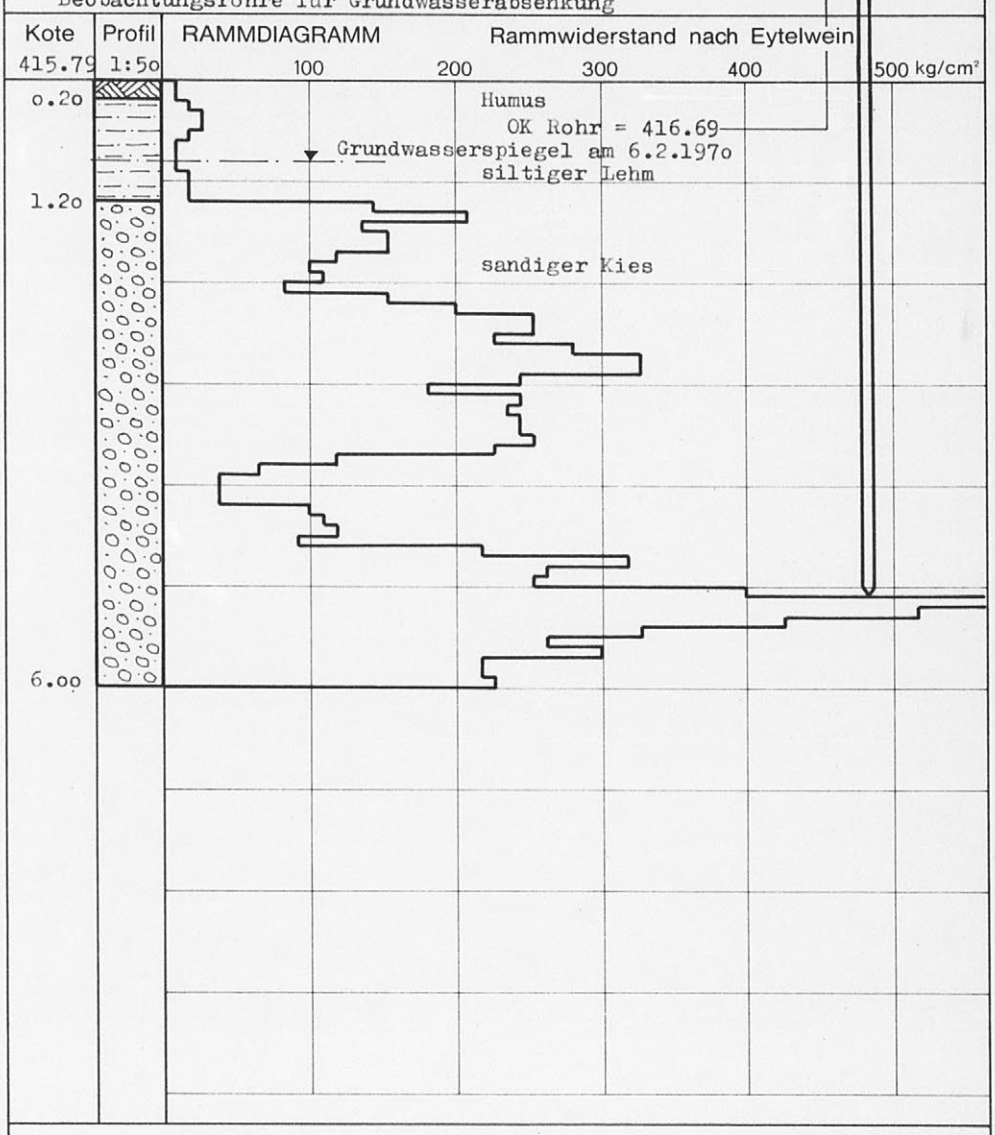

Rammgewicht: 45 kg
Fallhöhe: 20 cm
Spitzenquerschnitt: 10 cm²
Wasserstand: 1.7o m u.OK Rohr

7o717


Dr. Heinrich Jäckli
Geologe Zürich – Höngg
Limmattal-Strasse 289

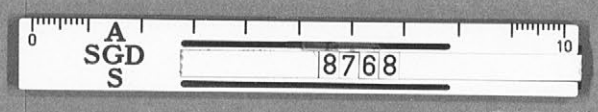

Baugrundsondierung No. 5

Objekt N 3, SBB Unterführung Lachen
Beobachtungsrohre für Grundwasserabsenkung


Datum: 6.2.197o

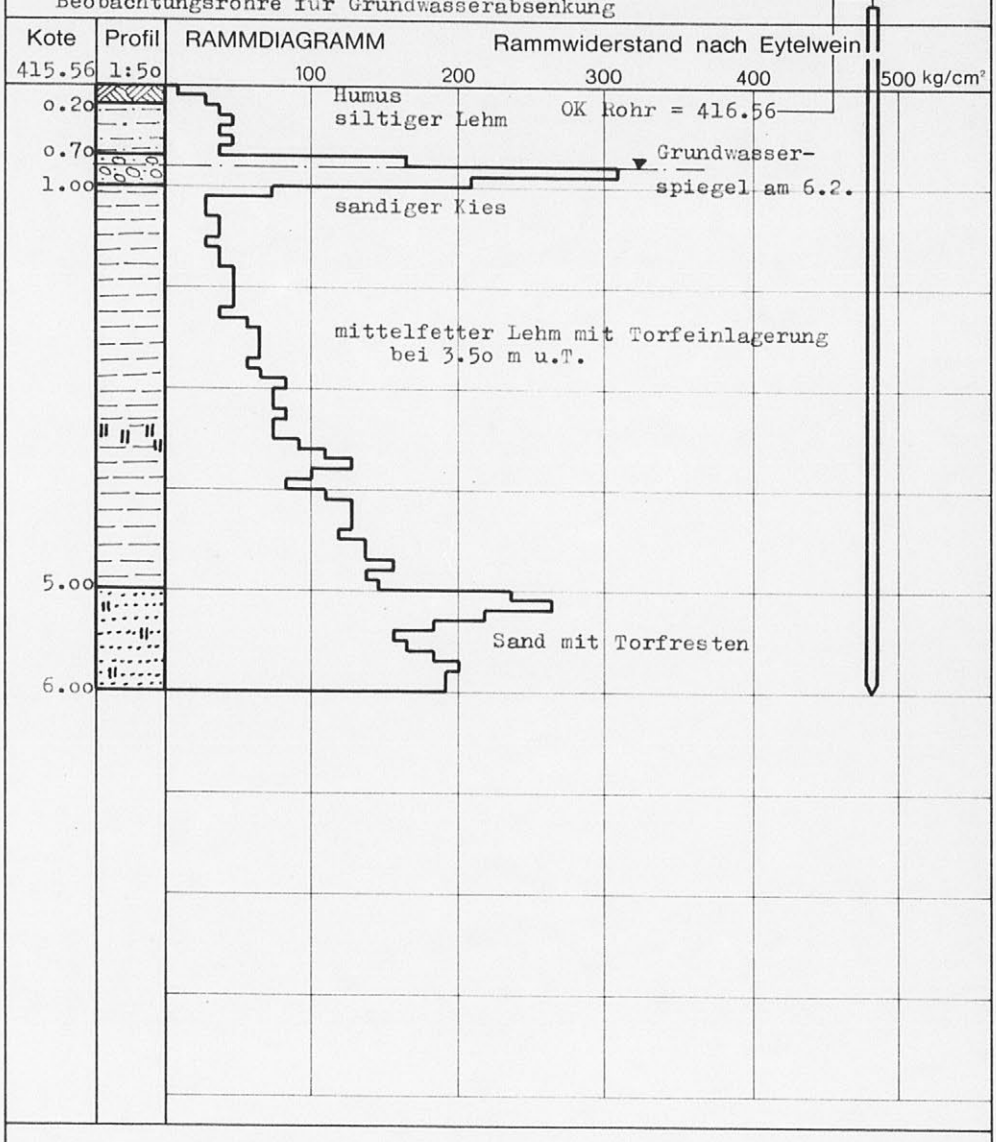

Rammgewicht: 45 kg
Fallhöhe: 20 cm
Spitzenquerschnitt: 10 cm²
Wasserstand: 1.8o m u.OK Rohr

Dr. Heinrich Jäckli
Geologe Zürich – Höngg
Limmattal-Strasse 289


7o717

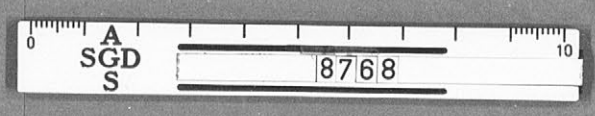

Baugrundsondierung No. 6

Objekt N 3, SBB Unterführung Lachen
Beobachtungsrohre für Grundwasserabsenkung


Datum: 29.1.197o

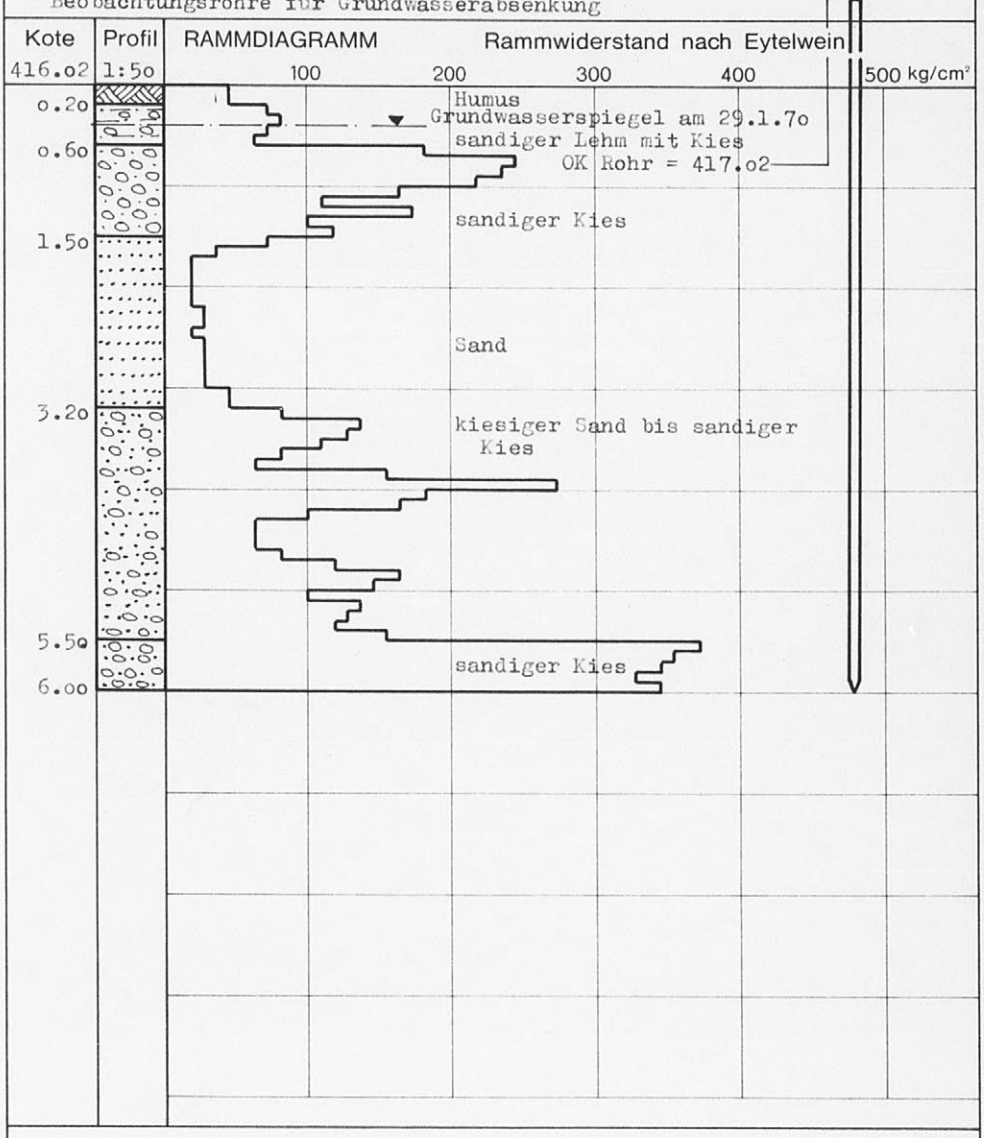

Rammgewicht:	45 kg
Fallhöhe:	20 cm
Spitzenquerschnitt:	10 cm²
Wasserstand:	1.4o m u.OK Rohr

Dr. Heinrich Jäckli
Geologe Zürich – Höngg
Limmattal-Strasse 289


7o717

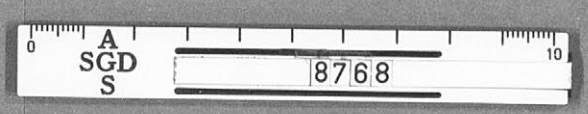

Baugrundsondierung No. 7

Objekt N 3, SBB Unterführung Lachen
Beobachtungsrohre für Grundwasserabsenkung

Datum: 4.3.197o

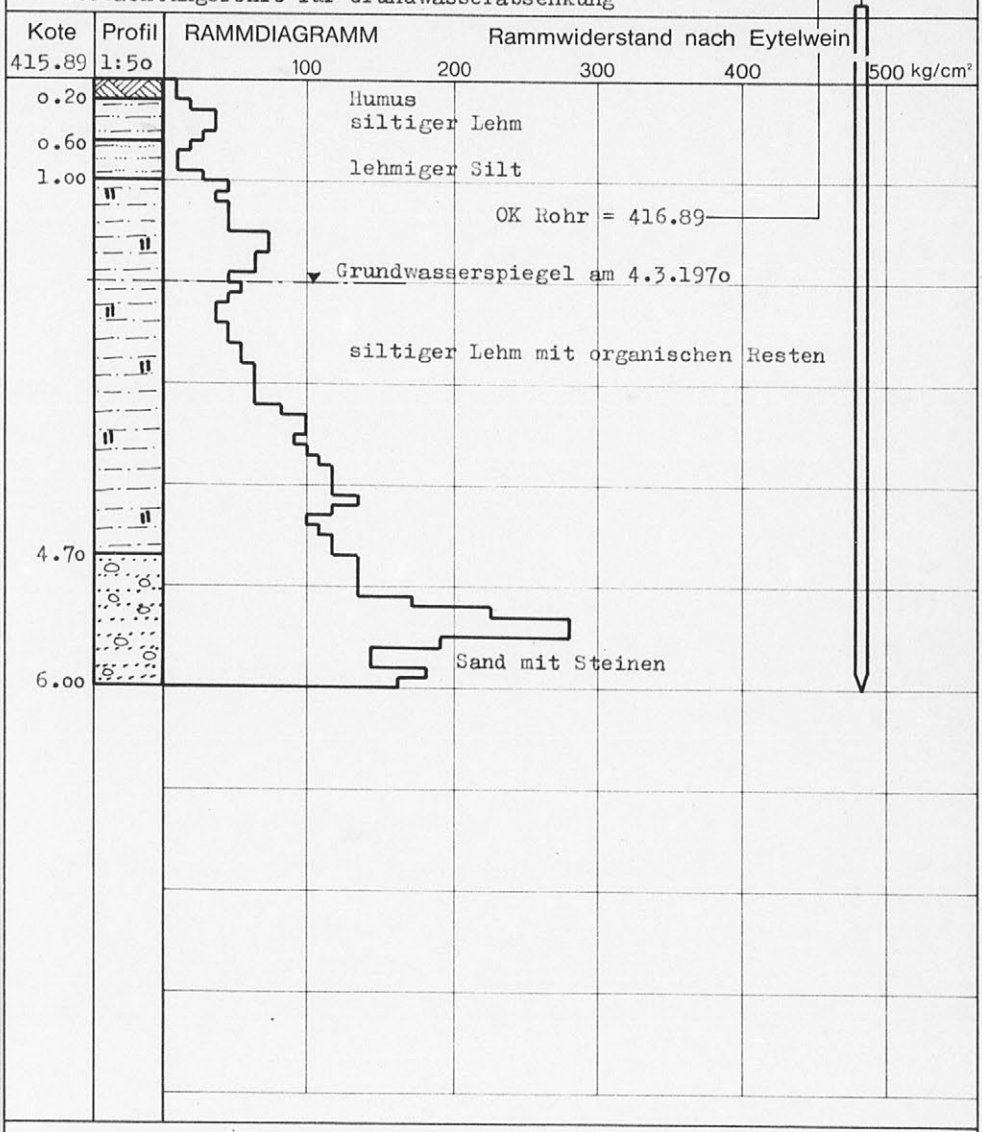

Rammgewicht:	45 kg	
Fallhöhe:	20 cm	
Spitzenquerschnitt:	10 cm²	
Wasserstand:	2.oo m u.OK Rohr	

7o717


Dr. Heinrich Jäckli
Geologe Zürich – Höngg
Limmattal-Strasse 289

0 A SGD S 10
8768

Baugrundsondierung No. 8

Objekt N 3, SBB Unterführung Lachen
Beobachtungsrohre für Grundwasserabsenkung

Datum: 4.3.197o

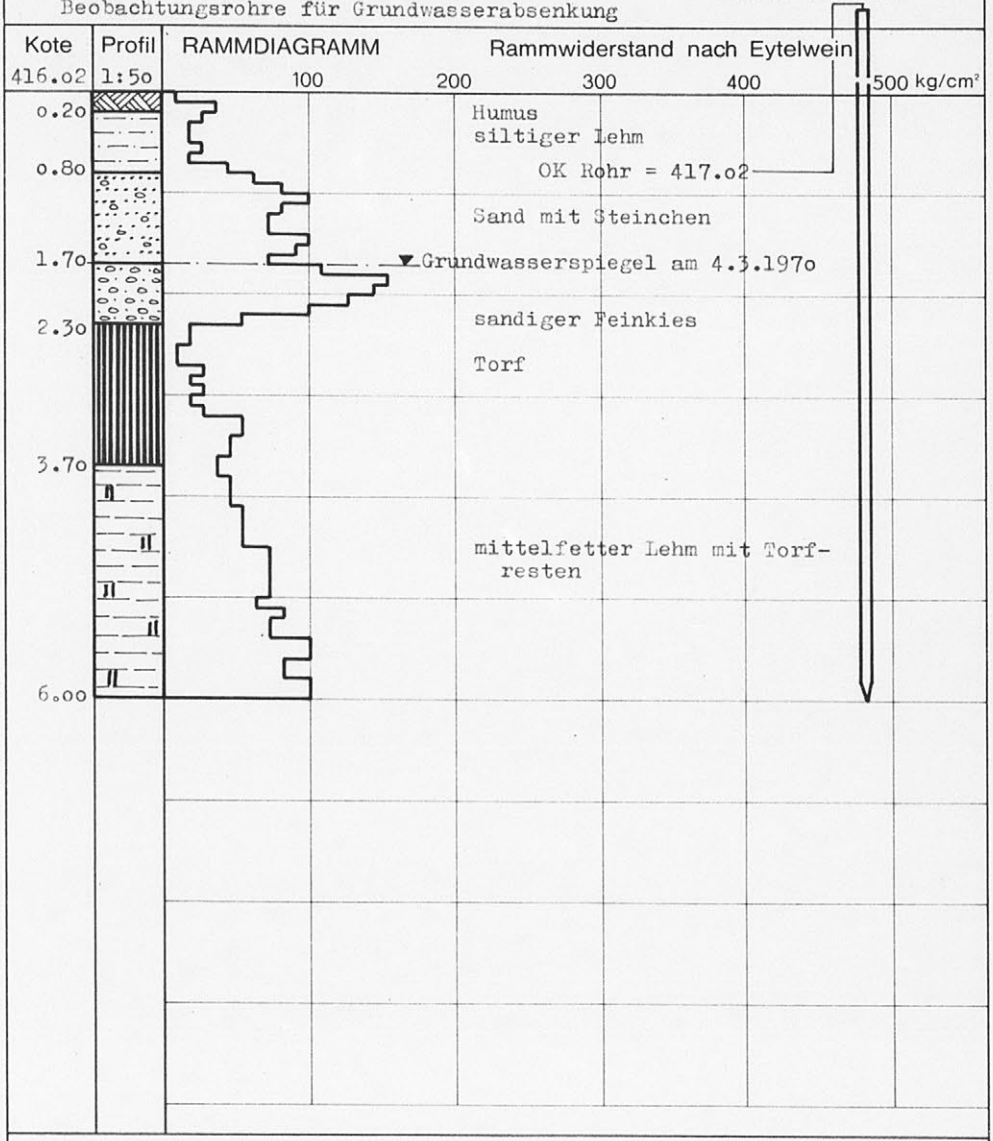

Rammgewicht:	45 kg	
Fallhöhe:	20 cm	
Spitzenquerschnitt:	10 cm²	
Wasserstand:	1.7o m u.OK Rohr	

7o717

Dr. Heinrich Jäckli
Geologe Zürich – Höngg
Limmattal-Strasse 289

