B E L E G B L A T T 2/2

SGD-Nr. Titel	14366 (1–7)	RA 01 02 03 (10)									Selektion (75) 1. 2. 3. 4. (76 82 90) Mut.
SGD-Nr. 1–7											
Anzahl Records (RA) 8	21	22	23	24							
Geologie 10 13 15	410 47 300	110 67 220	410 57 300	110 61 200							
Km-Netz 18 21	633 254	634 254	634 254	634 254							
Kartenblatt 24	1068	1068	1068	1068							
Verfügbarkeit 28	85										
Datum Autor(en) 30 37	0202976 (30)	Autor(en) MEN (37 41 45 49 53 57 61 65 69 73)									Mut. 3 (90)
Auftraggeber											

Verfalldatum: 31.12.1985

B E L E G B L A T T 1/2

SGD-Nr. Titel	14366 (1–7)	RA 01 SONDIERUNGEN FUER AUSBAU BAHNANLAGE TECKNAU 02 03 (10)									Selektion (75) 1. 14TEC 2. 3. 4. (76 82 90) Mut. 3
SGD-Nr. 1–7											
Anzahl Records [RA] 8	11	12	13	14	15	16	17	18	19	20	
Geologie 10 13 15	110 67 220	410 57 300	410 47 300	110 61 220	110 67 220	410 57 300	410 47 300	110 61 220	110 67 220	410 57 300	
Km-Netz 18 21	632 256	632 256	632 256	632 256	633 255	633 255	633 255	633 255	633 254	633 254	
Kartenblatt 24	1068	1068	1068	1068	1068	1068	1068	1068	1068	1068	
Verfügbarkeit 28	85										
Datum Autor(en) 30 37	0202976 (30)	Autor(en) MEN (37 41 45 49 53 57 61 65 69 73)									Mut. 3 (90)

Verfalldatum: 31.12.1985

Auftraggeber oder Rechtsnachfolger: SBB Kreis II, Luzern

Dokumentzusammensetzung:


Bericht	Notiz	Anzahl Seiten	Graphika, als Beilage oder allein	Tafeln, Abbildungen	Tabelle	Diagramme	Fotografien	Situationen 1:1000	geol.Bohrprofile 1:50 Tiefen: 15,00–30,00m	Rammprofile 1:100 Tiefen: 2,44–10,39m
			20					2	6	14

Originalkennzeichen des Dokumentes:

75.652 -1 bis -6
7-20

Geograph.Lage: *[Koordinaten]* *[oder Gebiet]*

EB

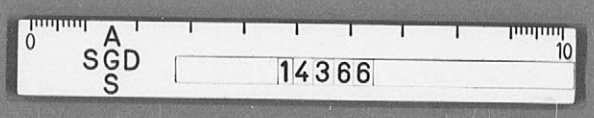

Strecke Basel - Olten

75.652

Km 26.160 - 26.750 (27.400)

Verbesserung der Fahrbahn

PLAN MIT SONDIERSTELLEN

M 1:1000

o Sondierbohrungen

• Rammsondierungen

Km 26.0 | 26.1 | 26.2 | 26.3 | 26.4

Wasserführung 3.60 m brt 3.50 m/t Zementrohre 045 m/t

Zementrohre 045 m/t

Zementrohre

Parallelweg 3.50 m brt

Erndhalde

Wolfst

R=753,8 m
R=750 m
U=135 mm

Z 120 m
A 300 m

UA 1.3
UA 1.4
UE 1.3
UE 1.4
UM
UM

PP28: 632.658,897 256.463,552 H= 425,948

PP27: 632.718,505 256.495,244 H= 426,895

PP29: 632.587,794 256.489,692 H= 425,249

632.820

256.300

632.500

632.474,248 256.533,483

Hpt. Lg. Elektra Ba L

Tb II / Schü Wa 30.6.75

A SGD S 14366

26.4

26.5

26.6

26.7

26.8

Zementfabrik

Strassenunterführung

Gde. Gelterkinden

Gde. Tecknau

Rüttihubelstr.

Wolfstige

Eibach

Kanalisationsüs SBR Ø 60cm

Zementrohre Ø 45 cm

Zementrohre Ø 30 cm

Sig. 1310

UE 2.3
UE 2.4
UA 2.3
UA 2.4
UM
Z 120
A 300

parallelweg 3.0 m brt

R=753,8 m
R=750 m
U=135 mm

BM
BM

PP27: 632.718,545 / 256.435,244 / H= 426,885

PP26: 632.788,011 / 256.388,813 / H= 427,618

Sig. 1310: 632.762,55 / 256.339,73 / H=

PP25: 632.847,866 / 256.331,986 / H= 428,461

PP24: 632.902,049 / 256.259,411 / H= 429,424

PP23: 632.947,003 / 256.191,564 / H= 430,020

PP22: 632.975,714 / 256.146,931 / H= 430,700

PP21: 633.037,929 / 256.052,030 / H= 431,834

632.600 · 256.300 · 632.700 · 256.200 · 632.800 · 256.100 · 632.900 · 256.000

1914 · 1915 · 1917 · 1918 · 1919 · 1921 · 1922


420 · 425 · 309 · 310 · 311 · 315 · 316 · 2035

52 · 53 · 54 · 55

SGD S A

0 10

14366

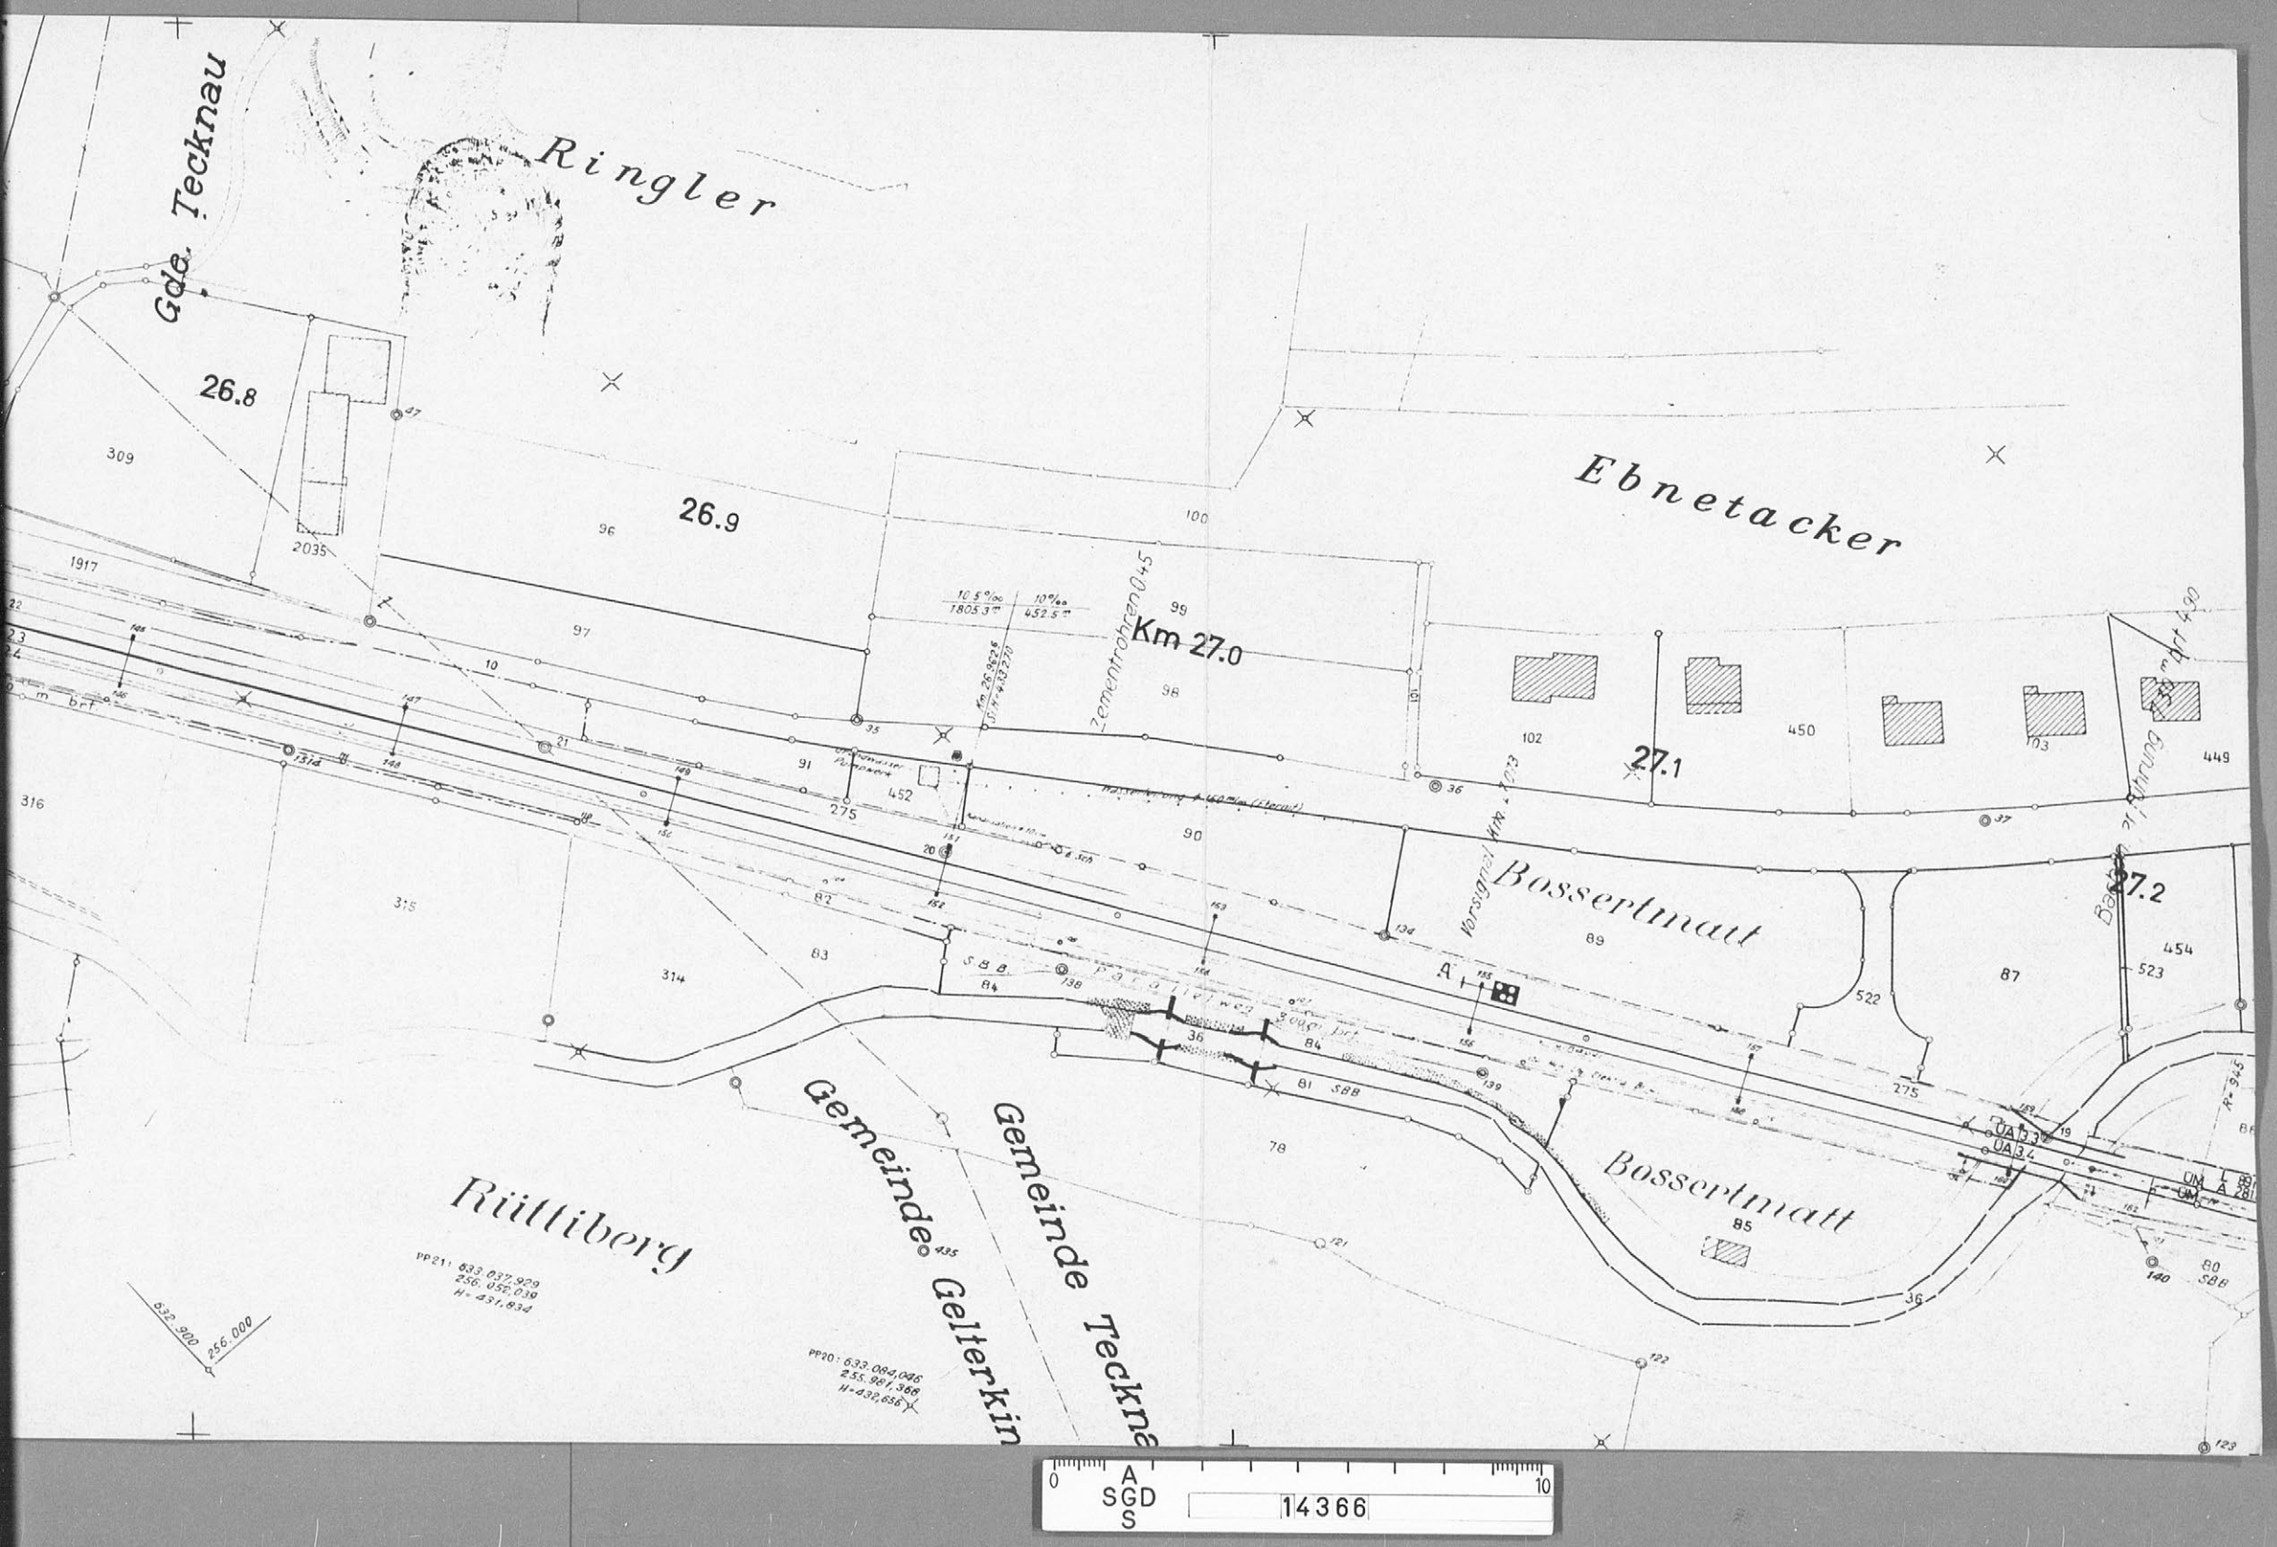
Gde. Tecknau
Ringler
26.8
26.9
Km 27.0
27.1
27.2
Ebnetacker
Bosserlmatt
Bosserlmatt
Rütliberg
Gemeinde Gelterkinden
Gemeinde Tecknau
Zementrohren 0.45
Vorsignal Km +1.23
SBB
Gemeinde
Bahnhof
UA 3.3
UA 3.4
PP21: 633.037.929
256.052.039
H= 431.834
PP20: 633.094.046
255.961.366
H=432.656
632.900
256.000
0
A
SGD
S
10
14366

Plan V

Strecke Basel-Olten

Km 27.400 (26.750)-28.850

75.652

Ausbau der Station Tecknau

PLAN MIT SONDIERSTELLEN

M1:1000

o Sondierbohrungen

• Rammsondierungen

Ringler

Gde. Gelterkinden

Gde. Tecknau

Ebnetacker

Bossertmatt

Bossertmatt

Km 27.0

26.8

26.9

27.1

Zementrohre Ø45 cm

Zementrohre Ø45 cm

Vorsignal Ank. Tecknau

Parallelweg 3.00 m breit

Parallelweg 3.00 m breit

UA 2.3

UA 2.4

UA 3.3

UA 3.4

SBB

Gemei

Gemei

Tb II/ Schü Wa 30.6.75


0 A SGD S 10

14366



0 A SGD S 10
14366


FÜR MIKROFILMAUFNAHME
UNGEEIGNETE VORLAGE

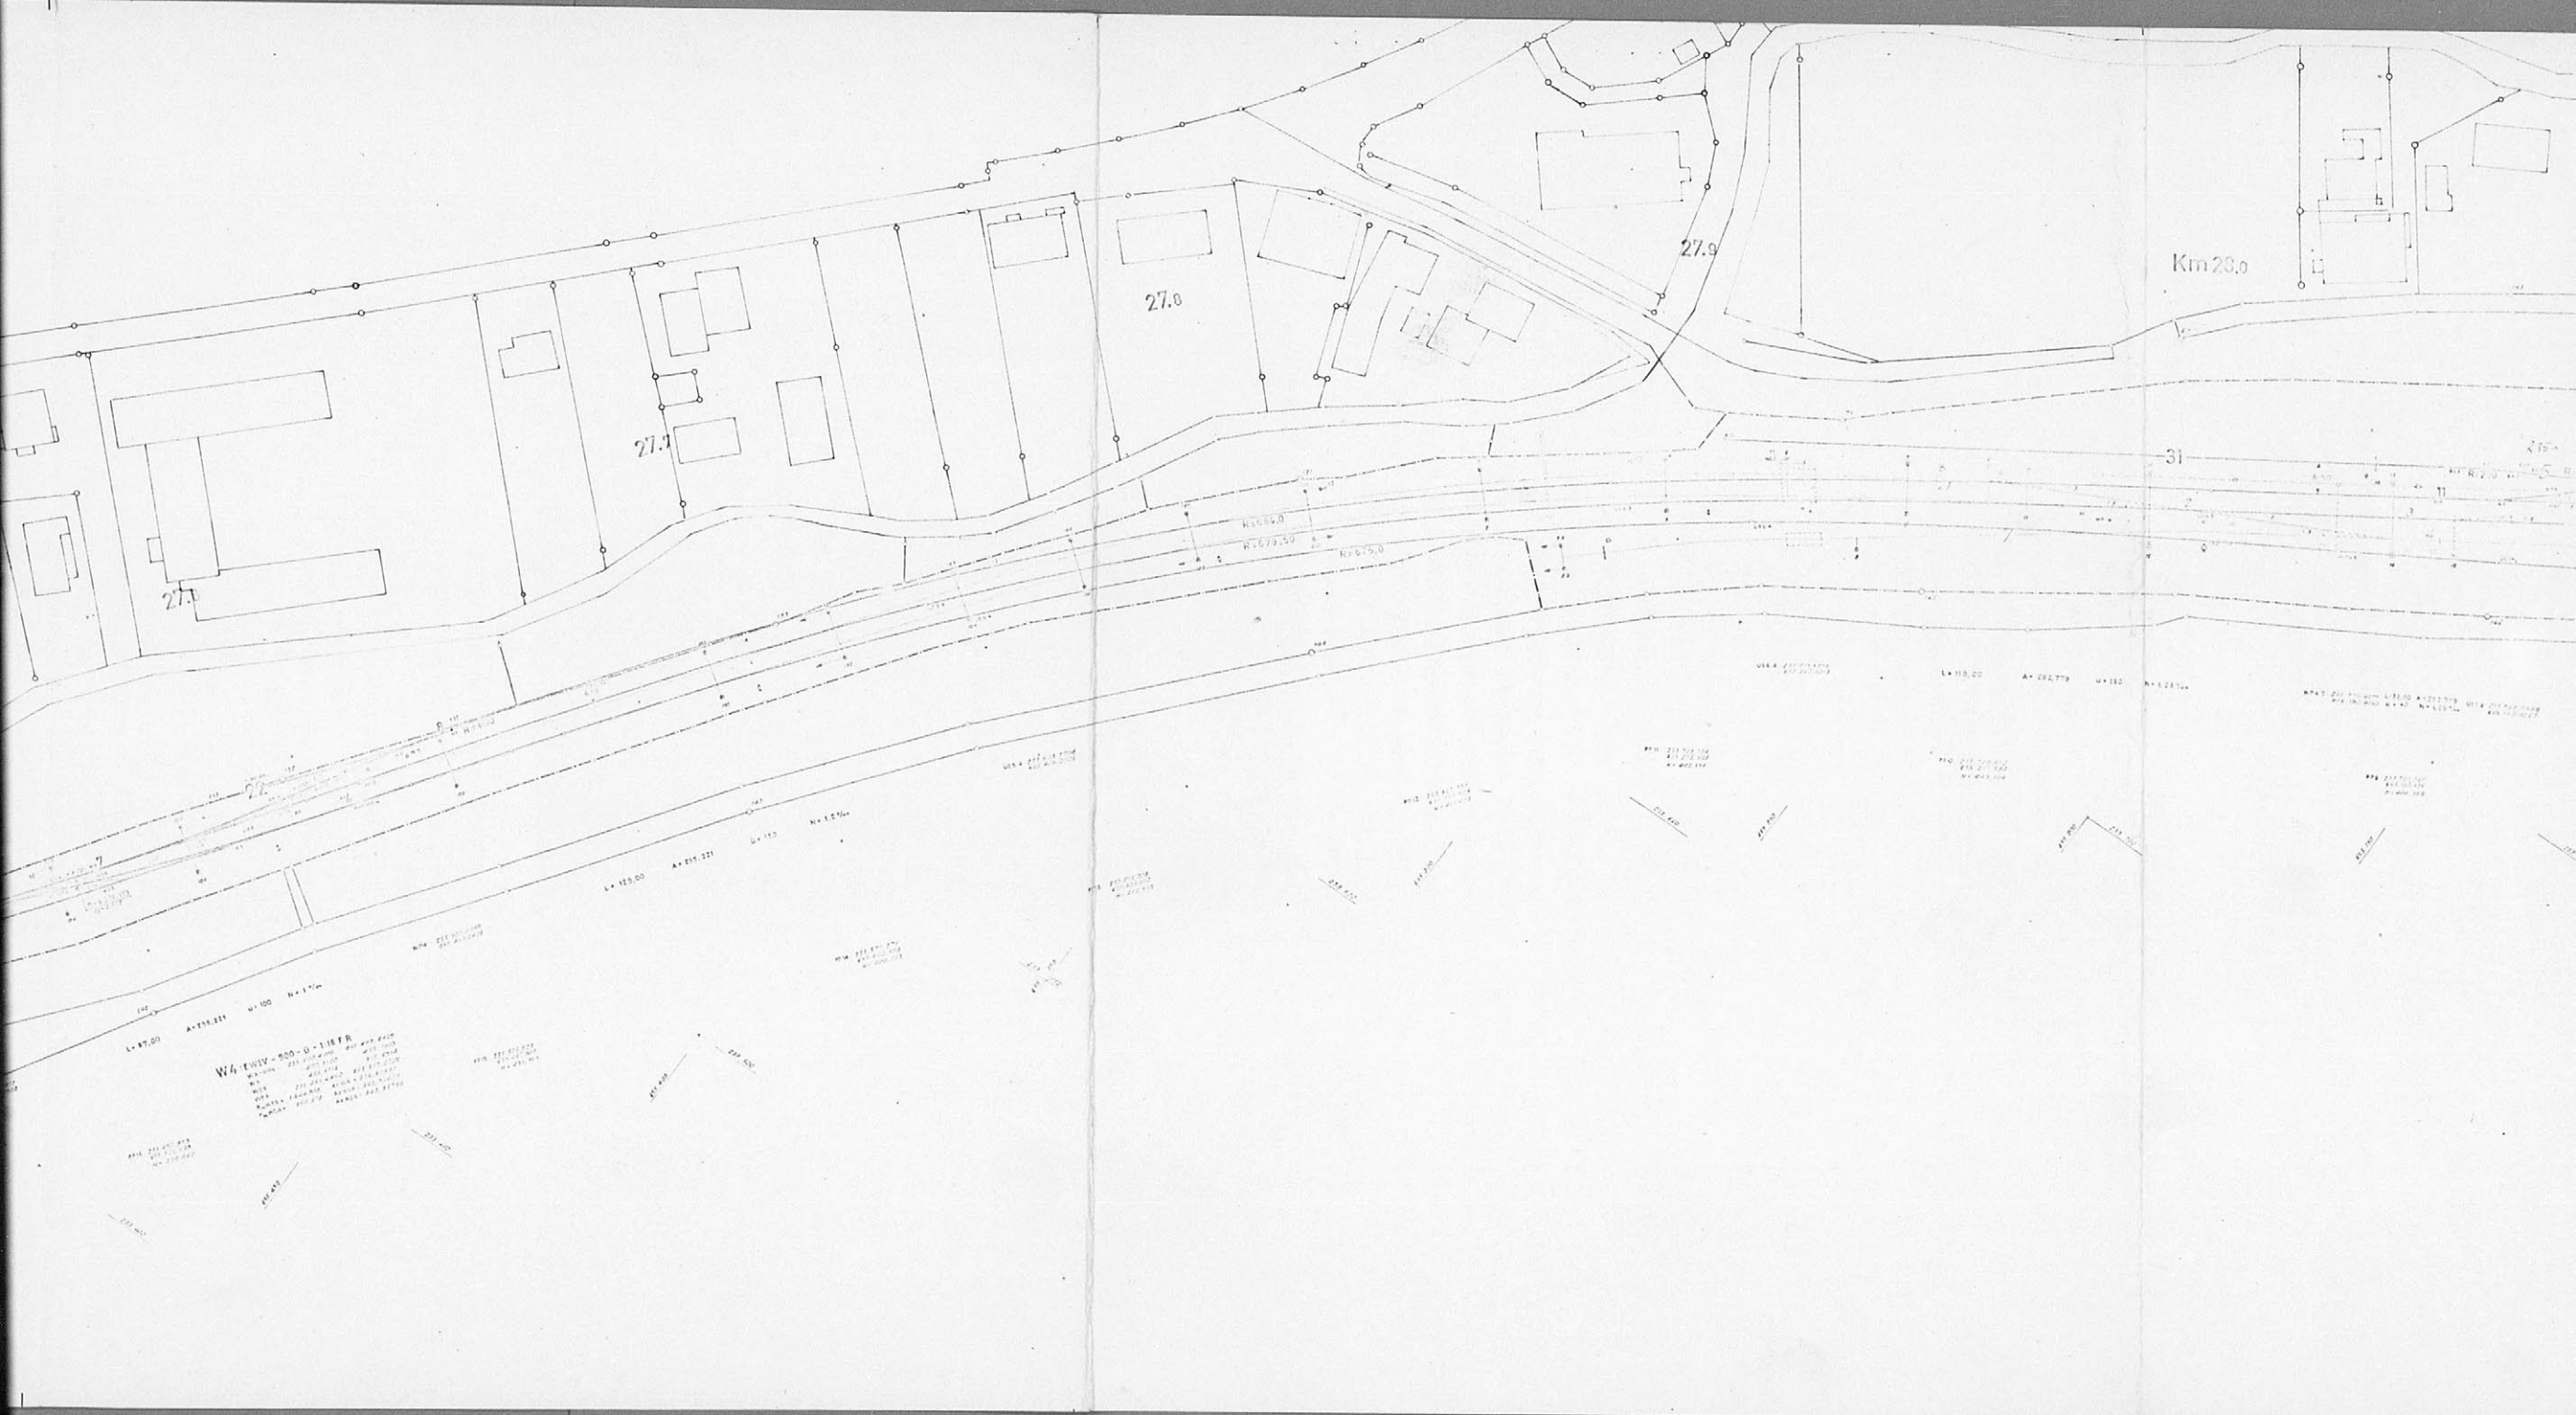

0 A SGD S 10
14366
FÜR MIKROFILMAUFNAHME
UNGEEIGNETE VORLAGE



A
SGD
S
14366
FÜR MIKROFILMAUFNAHME
UNGEEIGNETE VORLAGE

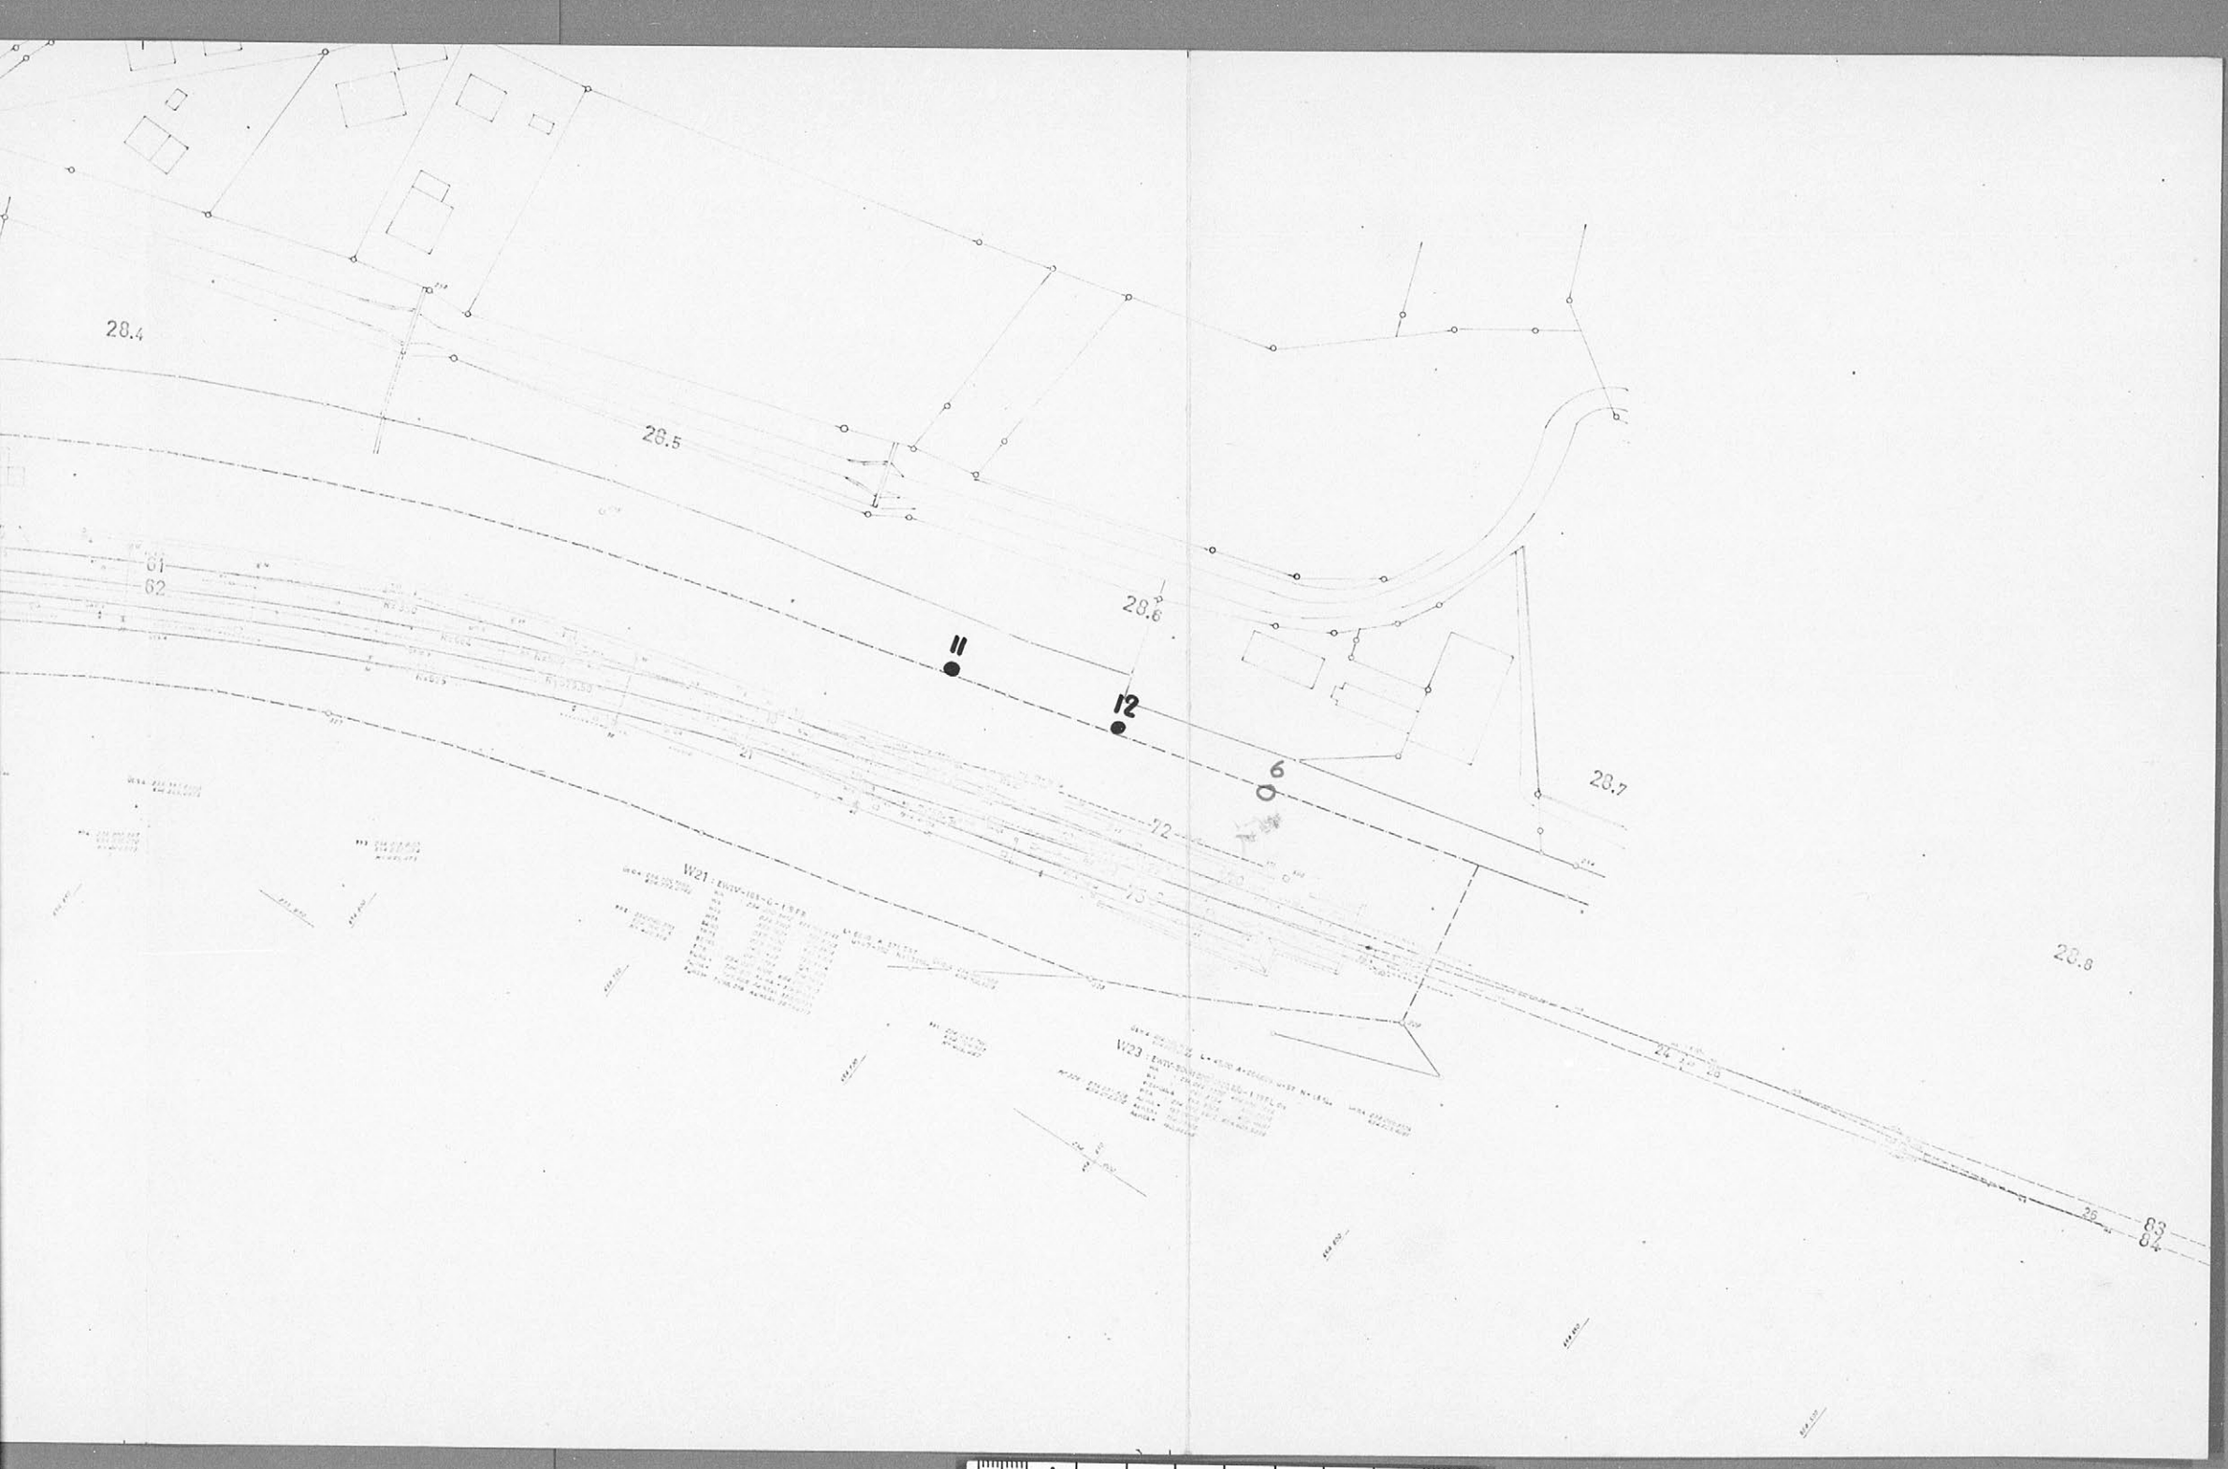

0 A SGD S 10
14366

FÜR MIKROFILMAUFNAHME
UNGEEIGNETE VORLAGE

BAUHERR: SBB, BAUABTEILUNG KREIS II, SEKT. TIEFBAU, LUZERN

OBJEKT: AUSBAU BAHNHOF UND BAHNANLAGE TECKNAU

SONDIERUNG Nr. SB 1

MASSTAB: 1 : 50

BERICHT:	BEILAGE:
LUZERN, 7. 1. 1976	GEZEICHNET: S. P.
PLAN Nr.: 75 652-1	FORMAT: 30 X 60
MEERESHÖHE: 424.88	KOORD: 632 865 / 256 280
AUSFÜHRUNGS-DATUM: 5. 12. 75 – 10. 12. 75	BOHRMEISTER: PORTMANN
PROFIL AUFGENOMMEN DURCH: BÜRO DR. U. VOLLENWEIDER, ZÜRICH	

Gebr. Mengis Luzern

BOHRART + BOHR ø	HÖHEN ÜBER MEER	TIEFEN AB OK TERRAIN	SCHICHTSTÄRKE	PROFIL	BESCHREIBUNG DES AUFGESCHLOSSENEN BOHRGUTES	USCS	GEOLOGISCHE IDENTIFIKATION	KERN-AUSBEUTE	BEMERKUNGEN
ø 175 mm		0.20			HUMUS		Verwitterungszone		
		0.60			BRAUNER, TONIGER SILT				
		1.30			OCKER – BRAUNER, LEICHT TONIGER SILTIG – KIESIGER SAND				
		1.80			OCKER – BRAUNER STARK TONIG – SILTIGER KIES – SAND				
		2.60			BRAUN – GRAUER STARK TONIG – SILTIGER KIES – SAND MIT STEINEN				2.90–3.20 ● 39
		3.30			BRAUN – GRAUER TONIG, SILTIG – SANDIGER KIES MIT WENIG STEINEN				4.25 ▽ GW.-SP. 18. 12. 75
		8.40			BRAUN – GRAUER, LEICHT TONIGER, SILTIG – SANDIGER KIES MIT VEREINZELT STEINEN BIS ø 12 CM KIES KANTENGERUNDET BIS GUT GERUNDET		Bachablagerung		6.10–6.40 ● 45
ø 145 mm		10.45			BRAUN – GRAUER TONIGER, STARK SILTIG – KIESIGER SAND MIT WENIG STEINEN				9.10–9.40 ● 24
		12.90			DUNKELGRAUER – BLAUER TONIGER SILT, WEICH BIS STEIF PLASTISCH, WEICHER STARK TONIGER MERGELFELS		Mergelfels vorwiegend Opalinuston		12.30–12.60 ● 126
		15.00			DUNKELGRAUER – BLAUER, TONIG – SANDIGER SILT, WEICHER MERGELFELS				

PIEZOMETER ø 2"

TIEFE	-8.00 m
GELOCHTE ROHRE	4.00 m
VOLLROHRE	5.00 m
ÜBERSTAND	1.00 m

2.90 – 3.20 ● 39 STANDARD-PENETRATION-TEST (SCHLÄGE PRO 30 cm EINDRINGUNG)

0 A SGD S 10 14366

BAUHERR: SBB, BAUABTEILUNG KREIS II, SEKT. TIEFBAU, LUZERN

OBJEKT: AUSBAU BAHNHOF UND BAHNANLAGE TECKNAU

SONDIERUNG Nr. SB 2

MASSTAB: 1 : 50

BERICHT: 313 / A	BEILAGE: 3 A
LUZERN, 7. 1. 1976	GEZEICHNET: S. P.
PLAN Nr.: 75 652 - 2	FORMAT: 30 X 60
MEERESHÖHE: 444.48	KOORD: 655'538 / 233'392
AUSFÜHRUNGS-DATUM: 10. 12. 75 – 12. 12. 75	BOHRMEISTER: PORTMANN
PROFIL AUFGENOMMEN DURCH: BÜRO DR. U. VOLLENWEIDER, ZÜRICH	


Gebr. Mengis Luzern

BOHRART + BOHR ø	HÖHEN ÜBER MEER	TIEFEN AB OK TERRAIN	SCHICHTSTÄRKE	PROFIL	BESCHREIBUNG DES AUFGESCHLOSSENEN BOHRGUTES	USCS	GEOLOGISCHE IDENTIFIKATION	KERN-AUSBEUTE	BEMERKUNGEN
ø 175 mm		0.70			GRAUER KIES, AUFFÜLLUNG		Dammschüttung		
		3.90			DUNKELGRAUER SILTIG – SANDIGER KIES MIT STEINEN, KIESIG – SANDIGE AUFFÜLLUNG				3.10 GW.-SP. 18.12.75 3.20-3.50 ● 8
		4.50			BRAUNER TONIGER SILT MIT KIES – SAND, AUFFÜLLUNG				
		5.10			BRAUNER TONIGER SILT MIT WENIG STEINEN (KANTIGER KALKSTEIN)				
ø 145 mm		6.40			BRAUNER TONIGER SILT MIT VEREINZELT KANTIGEN STEINEN (GEHÄNGELEHM), WEICH		Gehängelehm		6.00-6.30 ● 13
		7.60			BRAUNER TONIG – SANDIGER SILT MIT VIEL KANTIGEM KIES UND STEINEN (GEHÄNGELEHM), WEICH – MITTELHART, AB 7.50 M HÄRTER				
		10.40			BRAUN – GRAUER TONIG – SILTIG– SANDIGER KIES BIS TONIG – SANDIGER SILT MIT KIES, GEHÄNGESCHUTT (KIES, KANTIGER KALKSTEIN)		Gehängeschutt		9.10-9.40 ● 24
		12.70			DUNKELBRAUNER TONIG – SANDIGER SILT MIT REICHLICH KANTIGEM KIES, GEHÄNGESCHUTT				12.20-12.50 ● 26
ø 115 mm		13.60			OLIVGRAU – BLAUER TONIGER SILT, MIT WENIG KIES, VERWITTERTER MERGELFELS		Mergelfels (unterer Dogger)		
		16.50			DUNKELGRAU – BLAUER TONIGER SILT, WEICHER STARK TONIGER MERGELFELS				
		17.00			DUNKELGRAU – BLAUER TONIG – SANDIGER SILT, WEICHER MERGELFELS				

PIEZOMETER ø 2"

TIEFE	– 14.00 m
GELOCHTE ROHRE	6.00 m
VOLLROHRE	8.00 m
ÜBERSTAND	0

3.20 – 3.50 ● 8 STANDARD – PENETRATION – TEST (SCHLÄGE PRO 30cm EINDRINGUNG)

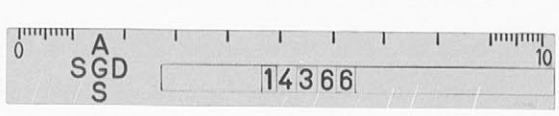

BAUHERR: SBB, BAUABTEILUNG KREIS II, SEKT. TIEFBAU, LUZERN

OBJEKT: AUSBAU BAHNHOF UND BAHNANLAGE TECKNAU

SONDIERUNG Nr. SB 3

MASSTAB: 1 : 50

BERICHT: 313 / B	BEILAGE: 3 B
LUZERN, 7. 1. 1976	GEZEICHNET: S. P.
PLAN Nr.: 75 652 – 3	FORMAT: 30 X 60
MEERESHÖHE: 445.09	KOORD: 655'106 / 233'865
AUSFÜHRUNGS-DATUM: 12. 12. 75 – 16. 12. 75	BOHRMEISTER: PORTMANN
PROFIL AUFGENOMMEN DURCH: BÜRO DR. U. VOLLENWEIDER, ZÜRICH	

Gebr. Mengis Luzern

BOHRART-BOHR ø	HÖHEN ÜBER MEER	TIEFEN AB OK TERRAIN	SCHICHTSTÄRKE	PROFIL	BESCHREIBUNG DES AUFGESCHLOSSENEN BOHRGUTES	USCS	GEOLOGISCHE IDENTIFIKATION	KERN-AUSBEUTE	BEMERKUNGEN
ø 175 mm		1.70			GRAUER KIES – SAND MIT STEINEN, AUFFÜLLUNG		Auffüllung		
		3.60			BRAUN – GRAUER SILTIG – SANDIGER KIES MIT VIEL STEINEN, GUT GERUNDET		Bachablagerung		3.10 – 3.40 / 3.45 ● 140 GW.-SP. 18.12.75
		7.20			BRAUN – GRAUER SILTIG – SANDIGER KIES MIT WENIG STEINEN, KIES VEREINZELT, GUT VERKITTET (BACHABLAGERUNG)				6.20 – 6.50 ● 72
		8.15			BRAUN – GRAUER SILTIGER KIES – SAND MIT STEINEN (BACHABLAGERUNG)				
		8.40			BRAUNER, TONIGER SILT, STEIF, VERWITTERTER MERGELFELS		verwitterter Mergelfels		
ø 145 mm		9.35			OLIVBRAUN – GRAUER TONIGER SILT, STEIF, VERWITTERTER MERGELFELS				9.20 – 9.50 ● 75
		11.40			DUNKELGRAU – BLAUER TONIGER SILT, WEICHER STARK TONIGER MERGELFELS		Mergelfels (unterer Dogger)		
ø 115 mm		12.50			DUNKELGRAU – BLAUER TONIG – SANDIGER SILT, WEICHER MERGELFELS MIT VEREINZELT SEHR WEICHEN ZONEN				11.60
		13.60			DUNKELGRAU – BLAUER MERGELFELS, WEICH BIS MITTELHART				BOHREN MIT DOPPELKERNROHR
		13.95			DUNKELGRAUER SILTSTEIN, MITTELHART BIS HART				
		15.00			DUNKELBLAU – GRAUER HORIZONTAL GESCHICHTETER MERGELFELS, MITTELHART MIT VEREINZELT WEICHEN ZONEN				15.00

PIEZOMETER ø 2"

TIEFE	– 6.00 m
GELOCHTE ROHRE	4.00 m
VOLLROHRE	2.00 m
ÜBERSTAND	0

3.10 – 3.40 ● 140 STANDARD – PENETRATION – TEST
(SCHLÄGE PRO 30 cm EINDRINGUNG)

0 A SGD S 10 14366

A SGD S 14366

BAUHERR: SBB, BAUABTEILUNG KREIS II, SEKT. TIEFBAU, LUZERN

OBJEKT: AUSBAU BAHNHOF UND BAHNANLAGE TECKNAU

SONDIERUNG Nr. SB 4

MASSTAB: 1:50

BERICHT: 313 / B	BEILAGE: 3 B
LUZERN, 2.2.1976	GEZEICHNET: E.H.
PLAN Nr.: 75 652 - 4	FORMAT: 30 x 88
MEERESHÖHE: 465.07	KOORD: 655'102 / 233'770
AUSFÜHRUNGS-DATUM: 14.1.1976 - 20.1.1976	BOHRMEISTER: PORTMANN
PROFIL AUFGENOMMEN DURCH: BÜRO DR.U. VOLLENWEIDER, ZÜRICH	

Gebr. Mengis Luzern

BOHRART + BOHR ø	HÖHEN ÜBER MEER	TIEFEN ± 0. AB OK TERRAIN	SCHICHTSTÄRKE	PROFIL	BESCHREIBUNG DES AUFGESCHLOSSENEN BOHRGUTES	USCS	GEOLOGISCHE IDENTIFIKATION	KERN-AUSBEUTE	BEMERKUNGEN
		0.40			HUMUS				
ø 200 mm		2.50			BRAUNER TONIGER SILT MIT KIES - SAND UND BLÖCKEN, GEHÄNGELEHM		Gehängeschutt		
		3.40			GRAU - BRAUNER TONIGER SILT, LEICHT SANDIG		Gehängelehm		3.00-3.30 ● 18
		4.60			BRAUN VERWITTERTE SANDIGE KALKSTEINBLÖCKE				
		5.20			BRAUN - BEIGER TONIG - SANDIGER SILT MIT EINZELNEN STEINEN				
		5.90			OLIV - GRAUBRAUNER TONIG - SANDIGER SILT (VERWITTERTER MERGEL) WEICH				
		6.80			DUNKELGRAUER STARK TONIGER MERGEL, WEICH				6.20-6.50 ● 32
		7.10			GRAUER LEICHT TONIG - SANDIGER KALK MIT FLASERIGEN TONEINLAGEN, LEICHT BRÄUNLICH ANGEWITTERT, MITTELHART				
		9.10			GRAUER SANDIGER KALK HART MIT EINZELNEN DUNKLEREN, MERGELIGEN ZWISCHENLAGEN				
		9.30			GRAU - BRAUNER TONIG - SANDIGER SILT, WEICH (KLUFTFÜLLUNG ODER VERRUTSCHTER FELS ?)				
		9.95			GRAUER SANDIGER KALK MIT STEILEN KLUFTEN, LEICHT BRÄUNLICH ANGE-WITTERT, MITTELHART BIS HART				
		10.00			GRAU - BRAUNER TONIG - SANDIGER SILT, WEICH (KLUFTFÜLLUNG ?)				
		10.40			DUNKELGRAU - BRAUNER MERGELIGER SANDSTEIN, WEICH BIS MITTELHART				
		10.70			OLIV- GRAUBRAUNER LEICHT SANDIG - TONIGER SILT (ANGEWITTERTER MERGEL)				
		12.20			DUNKELGRAUER LEICHT SANDIGER MERGEL, GESCHICHTET , WEICH BIS Z.T. MITTELHART		Verrutschter Mergelfels		
		13.40			DUNKELGRAU - SCHWARZER, UNREGELMÄSSIG GESCHICHTETER LEICHT SANDIGER MERGEL, WEICH				
		13.80			BRAUN - GRAUER SANDIGER MERGEL, WEICH MIT Z.T. SEHR WEICHEN LAGEN				
		14.50			GRAUER SANDIGER KALKSTEIN, GEKLÜFTET, HART				14.20 GW SP 23.1.1976
		15.20			DUNKELGRAUER MERGELIGER KALKSTEIN, MITTELHART GEGEN UNTEN BRECCIO				
		15.70			GRAUER TONIGER SILT MIT STEINEN (VERRUTSCHT?)				
ø 115 mm		20.20			DUNKELGRAU - SCHWARZE GESCHICHTETE WECHSELND TONIG - SANDIGE MERGEL MIT WEICHEN ZONEN VON 17.50 M BIS 18.90 M, RELATIV HOMOGEN		Mergelfels (unterer Dogger)		
		20.35			GRAUER SANDIGER KALKSTEIN				
		21.10			GRAUER TONIGER SILT				
					GRAUER SANDIGER KALK MIT MERGELIGEN EINLAGERUNGEN, ROSTIGE KLÜFTE				
					DUNKELGRAUE GESCHICHTETE WECHSELND SANDIG, LEICHT KALKIGE MERGEL WEICH BIS MITTELHART				

Ø 115 mm

15.70

GRAUER TONIGER SILT MIT STEINEN (VERRUTSCHT?)

DUNKELGRAU ~ SCHWARZE GESCHICHTETE WECHSELND TONIG ~ SANDIGE MERGEL MIT WEICHEN ZONEN VON 17.50 M BIS 18.90 M, RELATIV HOMOGEN

20.20

20.45

20.50

GRAUER SANDIGER KALKSTEIN

GRAUER TONIGER SILT

GRAUER SANDIGER KALK MIT MERGELIGEN EINLAGERUNGEN, ROSTIGE KLÜFTE

21.10

DUNKELGRAUE GESCHICHTETE WECHSELND SANDIG, LEICHT KALKIGE MERGEL WEICH BIS MITTELHART

24.00

DUNKELGRAU ~ SCHWARZE GESCHICHTETE WECHSELND TONIG ~ SANDIGE MERGEL, WEICH BIS MITTELHART, MIT WEICHEN STELLEN BEI ± 24.40 M BIS 24.90 M, 26.70 M BIS 27.00 M

30.00


Mergelfels (unterer Dogger)

Mergelfels

PIEZOMETER Ø 2"

TIEFE	-16.00m
GELOCHTE ROHRE	6.00m
VOLLROHRE	11.00m
ÜBERSTAND	1.00m

3.00 - 3.30 ●18 STANDARD - PENETRATION - TEST (SCHLÄGE PRO 30 cm EINDRINGUNG)

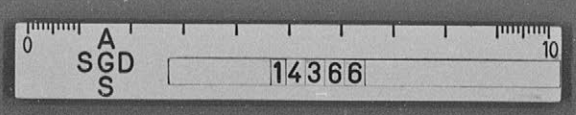

A SGD S 14366

BAUHERR: SBB, BAUABTEILUNG KREIS II, SEKT. TIEFBAU, LUZERN

OBJEKT: AUSBAU BAHNHOF UND BAHNANLAGE TECKNAU

SONDIERUNG Nr. SB 5

MASSTAB: 1:50

BERICHT: 313 / B	BEILAGE: 3 B
LUZERN, 2. 2. 1976	GEZEICHNET: E.H.
PLAN Nr.: 75 652 - 5	FORMAT: 30 x 80
MEERESHÖHE: 463.19	KOORD: 655'007 / 233'835
AUSFÜHRUNGS-DATUM: 16. 12. 1975 - 14. 1. 1976	BOHRMEISTER: PORTMANN
PROFIL AUFGENOMMEN DURCH: BÜRO DR. U. VOLLENWEIDER, ZÜRICH	

Gebr. Mengis Luzern

BOHRART + BOHR ø	HÖHEN ÜBER MEER	TIEFEN AB OK TERRAIN	SCHICHTSTÄRKE	PROFIL	BESCHREIBUNG DES AUFGESCHLOSSENEN BOHRGUTES	USCS	GEOLOGISCHE IDENTIFIKATION	KERN-AUSBEUTE	BEMERKUNGEN
ø 200 mm		0.40			HUMUS				
		5.10			HELLBRAUN - BEIGER BINDIGER KIES - SAND MIT EINZELNEN BLÖCKEN (HELLGRAUER OOLITHKALK) BIS ø 20 CM, KANTIGES GESTEIN, GEHÄNGESCHUTT VON 4.00 BIS 5.10 M LEICHT RÖTLICH		Gehängeschutt		3.10 - 3.40 ● 27
		7.50			BRAUNBEIGER STARK BINDIGER TONIGER SAND BIS SANDIG - TONIGER SILT MIT EINZELNEN BLÖCKEN (GRAUER SANDIGER KALK) GEHÄNGELEHM		Gehängelehm		6.00 - 6.30 ● 41
		7.70			OLIVGRAUER TONIGER SILT (VERWITTERTER MERGEL), WEICH				
		8.00			DUNKELGRAUER LEICHT SANDIG - SILTIGER TON				
		8.50			BRAUNER TONIGER SILT MIT EINZELNEN MERGELBROCKEN, SEHR WEICH				
		10.60			DUNKLER OLIVBRAUNER UNREGELMÄSSIG GESCHICHTETER STARK TONIGER MERGEL, NACH UNTEN ZUNEHMEND DUNKLER, GANZE ZONE MIT BRÄUNLICHER ANWITTERUNG (9.00 BIS 9.30 M UND 10.00 BIS 10.20 M PROBE) WEICH BIS SEHR WEICH				9.10 - 9.40 ● 104
		10.90			OLIVBRAUNER LEICHT SANDIGER MERGEL, WEICH				
		11.30			EINZELNE MERGELIGE SANDKALKSTEINE, BRAUN, VERWITTERT IN BRAUNER BINDIGER GRUNDMASSE				
		11.50			PROBE				
		11.70			DUNKELGRAU - SCHWARZER, STARK TONIGER MERGEL, WEICH				
		12.00			GRAUER LEICHT SPÄTIGER SANDIGER KALK, HART				
		12.40			DUNKELGRAUER SANDIGER KALK, LEICHT SPÄTIG MIT SCHWARZEN FLASRIGEN TONEINSCHLÜSSEN, MITTELHART BIS HART				
		12.50			WIE OBEN MIT VIELEN SCHWARZEN TONEINSCHLÜSSEN, MITTELHART				
		12.65			WIE 12.00 BIS 12.40 M				
		13.00			BRAUNER TONIGER SILT MIT STEINEN BIS ø 10 CM, VORWIEGEND KALKSTEIN				
		13.55			DUNKELGRAU - SCHWARZER KALKIGER MERGEL MIT SANDKALK-ZWISCHENLAGEN, MITTELHART				
		13.90			OLIVGRAU - BRÄUNER MERGEL, WEICH				
		14.15			PROBE				
		14.60			DUNKELGRAU - SCHWARZER STARK TONIGER MERGEL, SEHR WEICH				
		15.10			DUNKELGRAU - SCHWARZER LEICHT SANDIG KALKIGER MERGEL, NACH UNTEN SANDIGER, LEICHT ZERKLÜFTET				
ø 115 mm		16.60			GRAU - BRÄUNLICH ANGEWITTERTER SANDIGER KALK MIT WENIG FLASRIGEN TONEINLAGEN, STELLENWEISE LEICHT HART, MIT RELATIV STEIL STEHENDEN KLÜFTEN		Verrutschter Mergelfels (unterer Dogger)		
		16.90			DUNKELGRAUER MERGELIG - SANDIGER KALK, MITTELHART - HART				
		18.40			GRAU Z.T. HELLGRAUER STARK SANDIGER KALK MIT MERGELIGEN ZWISCHENLAGEN, MITTELHART BIS HART				
		18.60			DUNKELGRAU MERGELIG - SANDIGER KALK, MITTELHART BIS HART				
		19.00			PROBE				
		20.00			DUNKELGRAU - SCHWARZER, UNREGELMÄSSIG FEIN GEBANKTER, LEICHT SANDIGER MERGEL, WEICH, EINZELNE STELLEN SEHR WEICH				
		20.25			PROBE				
		22.40			DUNKELGRAU - SCHWARZER, UNREGELMÄSSIG FEIN GEBANKTER, LEICHT SANDIGER MERGEL, WEICH BIS SEHR WEICH				
		23.25			HELLGRAUER STARK SANDIGER KALK, STEIL GEKLÜFTET, Z.T. BRÄUNLICH ANGEWITTERT, HART				
		23.65			DUNKELGRAUER SANDIG - KALKIGER MERGEL, WEICH BIS MITTELHART				

12.00 — BOHREN M. DOPPELKERNROHR — 14.00

GW.SP. 14. 1. 1976 12.80

10.90		OLIVBRAUNER LEICHT SANDIGER MERGEL, WEICH
11.30		EINZELNE MERGELIGE SANDKALKSTEINE, BRAUN, VERWITTERT IN BRAUNER BINDIGER GRUNDMASSE
11.50		PROBE
11.70		DUNKELGRAU - SCHWARZER, STARK TONIGER MERGEL, WEICH
12.00		GRAUER LEICHT SPÄTIGER SANDIGER KALK, HART
12.40		DUNKELGRAUER SANDIGER KALK, LEICHT SPÄTIG MIT SCHWARZEN FLASRIGEN TONEINSCHLÜSSEN, MITTELHART BIS HART
12.50		WIE OBEN MIT VIELEN SCHWARZEN TONEINSCHLÜSSEN, MITTELHART
12.65		WIE 12.00 BIS 12.40 M
13.00		BRAUNER TONIGER SILT MIT STEINEN BIS Ø 10 CM, VORWIEGEND KALKSTEIN
13.55		DUNKELGRAU - SCHWARZER KALKIGER MERGEL MIT SANDKALK- ZWISCHEN-LAGEN, MITTELHART
13.90		OLIVGRAU - BRAUNER MERGEL, WEICH
14.15		PROBE
14.60		DUNKELGRAU - SCHWARZER STARK TONIGER MERGEL, SEHR WEICH
15.10		DUNKELGRAU - SCHWARZER LEICHT SANDIG KALKIGER MERGEL, NACH UNTEN SANDIGER, LEICHT ZERKLÜFTET
16.60		GRAU - BRÄUNLICH ANGEWITTERTER SANDIGER KALK MIT WENIG FLASRIGEN TONEINLAGEN, STELLENWEISE LEICHT HART, MIT RELATIV STEIL STEHENDEN KLÜFTEN
16.90		DUNKELGRAUER MERGELIG - SANDIGER KALK, MITTELHART - HART
18.40		GRAU Z. T. HELLGRAUER STARK SANDIGER KALK MIT MERGELIGEN ZWISCHEN-LAGEN, MITTELHART BIS HART
18.60		DUNKELGRAU MERGELIG - SANDIGER KALK, MITTELHART BIS HART
19.00		PROBE
20.00		DUNKELGRAU - SCHWARZER, UNREGELMÄSSIG FEIN GEBANKTER, LEICHT SANDIGER MERGEL, WEICH, EINZELNE STELLEN SEHR WEICH
20.25		PROBE
22.40		DUNKELGRAU - SCHWARZER, UNREGELMÄSSIG FEIN GEBANKTER, LEICHT SANDIGER MERGEL, WEICH BIS SEHR WEICH
23.25		HELLGRAUER STARK SANDIGER KALK, STEIL GEKLÜFTET, Z. T. BRÄUNLICH ANGEWITTERT, HART
23.65		DUNKELGRAUER SANDIG - KALKIGER MERGEL, WEICH BIS MITTELHART
24.00		WIE 22.40 BIS 23.25 M
24.30		DUNKELGRAU - SCHWARZER, UNREGELMÄSSIG GESCHICHTETER MERGEL, WEICH
24.65		HELLGRAUER, SANDIGER KALK, HART
25.00		DUNKELGRAU - SCHWARZER, GESCHICHTETER LEICHT SANDIGER MERGEL, WEICH BIS MITTELHART

Ø 115 mm


Verrutschter Mergel

Mergelfels (unterer Dogger)

12.00 – 14.00 BOHREN M. DOPPELKERNROHR

GW. SP. 14.1.1976 12.80

3.10-3.40 ● 27 STANDARD-PENETRATION -TEST (SCHLÄGE PRO 30 cm EINDRINGUNG)

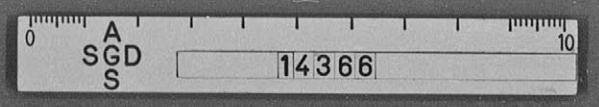

BAUHERR: SBB, BAUABTEILUNG KREIS II, SEKT. TIEFBAU, LUZERN

OBJEKT: AUSBAU BAHNHOF UND BAHNANLAGE TECKNAU

SONDIERUNG Nr. SB 6

MASSTAB: 1:50

BERICHT:	BEILAGE:
LUZERN, 2.2.1976	GEZEICHNET: E.H.
PLAN Nr.: 75 652 - 6	FORMAT: 30 x 62
MEERESHÖHE:	KOORD: 654'669/238'82
AUSFÜHRUNGS-DATUM: 20.1.1976 - 23.1.1976	BOHRMEISTER: PORTMANN
PROFIL AUFGENOMMEN DURCH: BÜRO DR. U. VOLLENWEIDER, ZÜRICH	

Gebr. Mengis Luzern

BOHRART + BOHR ⌀	HÖHEN ÜBER MEER	TIEFEN AB OK TERRAIN	SCHICHTSTÄRKE	PROFIL	BESCHREIBUNG DES AUFGESCHLOSSENEN BOHRGUTES	USCS	GEOLOGISCHE IDENTIFIKATION	KERN-AUSBEUTE	BEMERKUNGEN
⌀ 200 mm		0.30			HUMUS				
		1.70			BRAUNER TONIGER SILT MIT KANTIGEM KIES		Gehängeschutt (ev. Auffüllung ?)		3.10-3.40 ● 12
		2.10			BRAUNER LEICHT TONIG - SILTIGER KIES - SAND MIT KANTIGEN STEINEN (OOLITH)				
		4.75			BRAUNER TONIG - SANDIGER SILT MIT REICHLICH KANTIGEM KIES UND STEINEN				
		6.20			BRAUNER TONIGER SILT				6.00-6.30-6.35 ● 25 ▽ GW.SP 23.1.1976
		7.50			BRAUNER STARK BINDIGER KIES - SAND MIT WENIG STEINEN BIS ⌀ 12 CM KIES UND STEINE KANTENGERUNDET (JURASCHOTTER)		Bachablagerung		
⌀ 175 mm		12.80			BRAUNER BINDIGER SANDIGER KIES MIT STEINEN BIS ⌀ 15 CM, STEINE KANTENGERUNDET (JURASCHOTTER)				9.10-9.40 ● 108
		14.60			GRAUER SILTIG - SANDIGER KIES MIT REICHLICH STEINEN				12.00-12.25 ● 225 (25 cm)
⌀ 145 mm		15.00			OLIVBRAUN - GRAUER MERGEL, WEICH		Mergelfels		
		17.00			DUNKELGRAUER TONIGER LOKAL LEICHT SANDIGER MERGEL GEGEN UNTEN ZUNEHMEND TONIGER, WEICH BIS Z.T. SEHR WEICH (OPALINUSTON)				

PIEZOMETER ⌀ 2"

TIEFE	- 10.00 m
GELOCHTE ROHRE	4.00 m
VOLLROHRE	7.00 m
ÜBERSTAND	1.00 m


3.10-3.40 ● 12 STANDARD-PENETRATION-TEST (SCHLÄGE PRO 30 cm EINDRINGUNG)

0 A SGD S 10 14366

BAUHERR : SCHWEIZERISCHE BUNDESBAHNEN, BAUABTEILUNG KREIS II, SEKTION TIEFBAU, LUZERN

OBJEKT : AUSBAU BAHNHOF UND BAHNANLAGE TECKNAU

RAMMSONDIERUNG RS 1

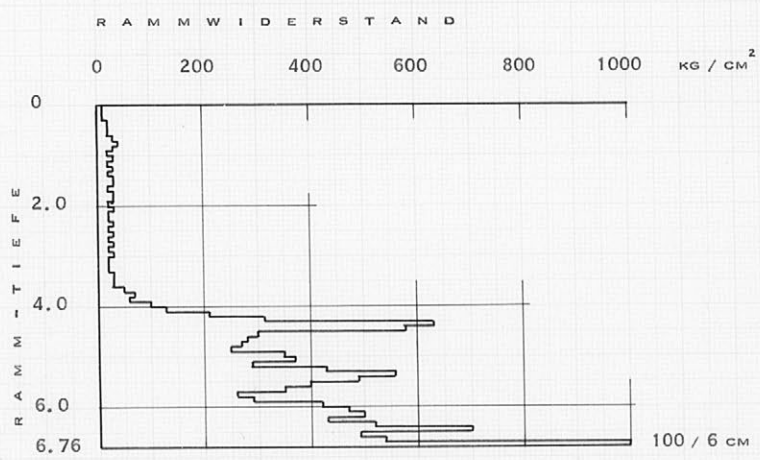

SCHWERE RAMMSONDE:

GESTÄNGE	ø	38 MM
SPITZE	F	30 CM²
BÄR	G	60 KG
FALLHÖHE	H	50 CM

. LUZERN, 23. 12. 1975
75 652 - 7 SP


BOHRUNTERNEHMUNG
GEBR. MENGIS . LUZERN

0 A SGD S 10
14366

BAUHERR : SCHWEIZERISCHE BUNDESBAHNEN, BAUABTEILUNG KREIS II, SEKTION TIEFBAU, LUZERN

OBJEKT : AUSBAU BAHNHOF UND BAHNANLAGE TECKNAU

RAMMSONDIERUNG RS 2

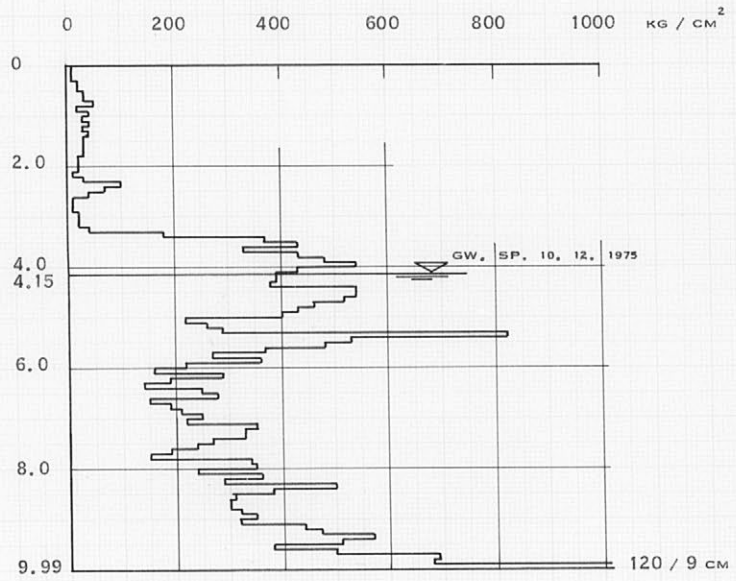

. LUZERN, 23. 12. 1975
75 652 - 8 SP


BOHRUNTERNEHMUNG
GEBR. MENGIS . LUZERN

0 A SGD S 10
14366

BAUHERR : SCHWEIZERISCHE BUNDESBAHNEN, BAUABTEILUNG KREIS II, SEKTION TIEFBAU, LUZERN

OBJEKT : AUSBAU BAHNHOF UND BAHNANLAGE TECKNAU

RAMMSONDIERUNG RS 3

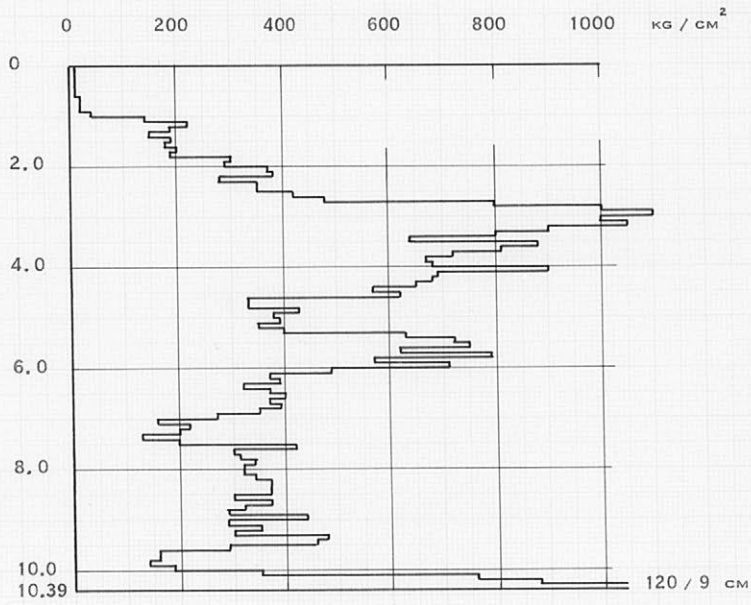

LUZERN, 23. 12. 1975
75 652 - 9 SP


BOHRUNTERNEHMUNG
GEBR. MENGIS LUZERN

0 A SGD S 10
14366

BAUHERR : SCHWEIZERISCHE BUNDESBAHNEN, BAUABTEILUNG KREIS II
SEKTION TIEFBAU, LUZERN

OBJEKT : AUSBAU BAHNHOF UND BAHNANLAGE TECKNAU

RAMMSONDIERUNG RS 4

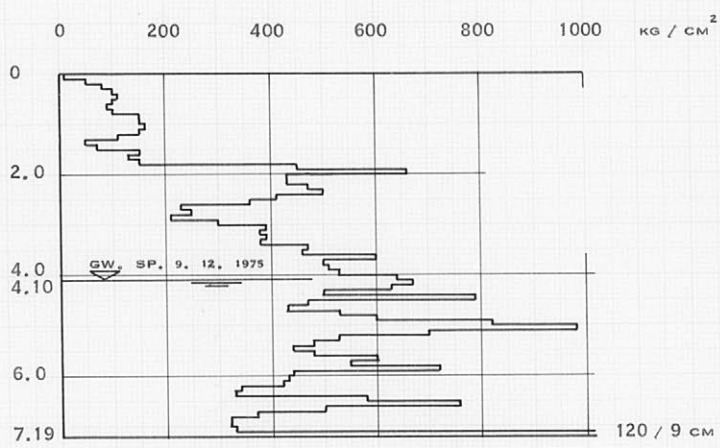

LUZERN, 23. 12. 1975
75 652 - 10 SP


BOHRUNTERNEHMUNG
GEBR. MENGIS LUZERN

0 A SGD S 10
14366

BAUHERR : SCHWEIZERISCHE BUNDESBAHNEN, BAUABTEILUNG KREIS II, SEKTION TIEFBAU, LUZERN


OBJEKT : AUSBAU BAHNHOF UND BAHNANLAGE TECKNAU

RAMMSONDIERUNG RS 5

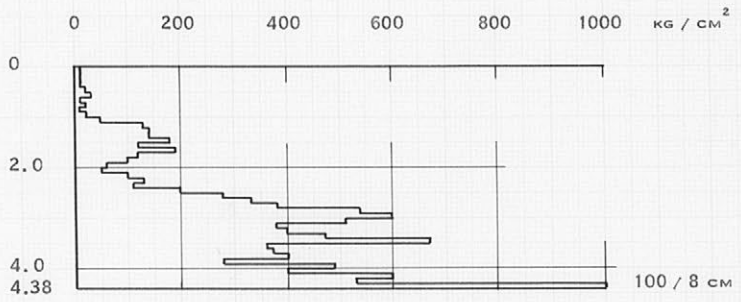

. LUZERN, 23. 12. 1975
75 652 - 11 SP


BOHRUNTERNEHMUNG
GEBR. MENGIS LUZERN

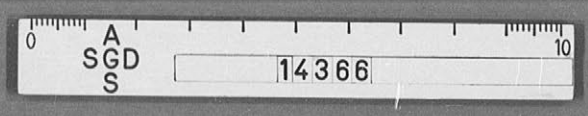

BAUHERR : SCHWEIZERISCHE BUNDESBAHNEN, BAUABTEILUNG KREIS II, SEKTION TIEFBAU, LUZERN

OBJEKT : AUSBAU BAHNHOF UND BAHNANLAGE TECKNAU

RAMMSONDIERUNG RS 6

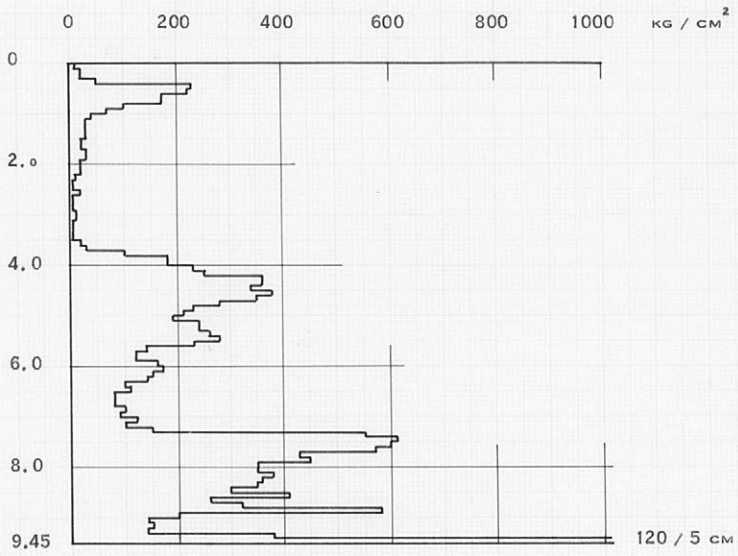

LUZERN, 23. 12. 1975
75 652 - 12 SP


BOHRUNTERNEHMUNG
GEBR. MENGIS LUZERN

0 ASGDS 10
14366

BAUHERR : SCHWEIZERISCHE BUNDESBAHNEN, BAUABTEILUNG KREIS II, SEKTION TIEFBAU, LUZERN

OBJEKT : AUSBAU BAHNHOF UND BAHNANLAGE TECKNAU

RAMMSONDIERUNG RS 7

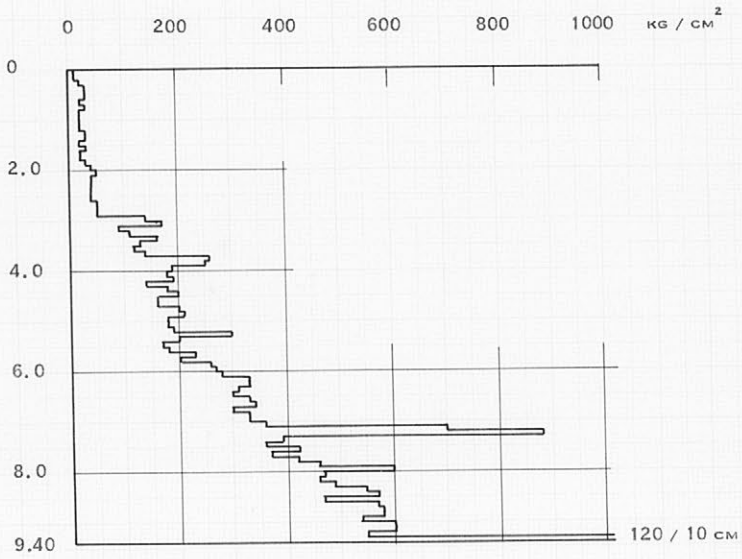

LUZERN, 23. 12. 1975
75 652 - 13 SP


BOHRUNTERNEHMUNG
GEBR. MENGIS LUZERN

0 A SGD S 10
14366

BAUHERR : SCHWEIZERISCHE BUNDESBAHNEN, BAUABTEILUNG KREIS II, SEKTION TIEFBAU, LUZERN

OBJEKT : AUSBAU BAHNHOF UND BAHNANLAGE TECKNAU

RAMMSONDIERUNG RS 7 A

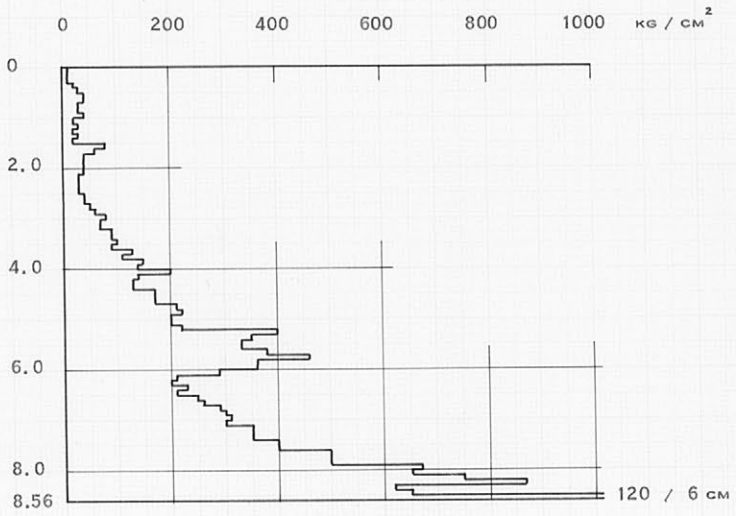

LUZERN, 23. 12. 1975
75 652 - 14 SP


BOHRUNTERNEHMUNG
GEBR. MENGIS LUZERN

0 ASGDS 10
14366

BAUHERR : SCHWEIZERISCHE BUNDESBAHNEN, BAUABTEILUNG KREIS II, SEKTION TIEFBAU, LUZERN

OBJEKT : AUSBAU BAHNHOF UND BAHNANLAGE TECKNAU

RAMMSONDIERUNG RS 8

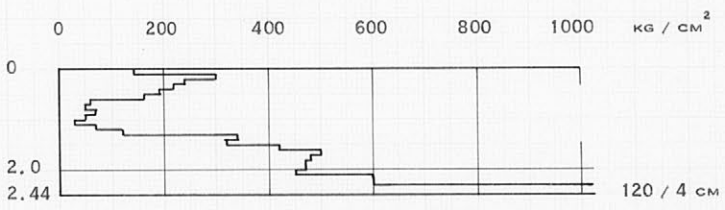

RAMMSONDIERUNG RS 8 A
(1.5 M VERSETZT)



LUZERN, 23. 12. 1975
75 652 - 15 SP


BOHRUNTERNEHMUNG
GEBR. MENGIS LUZERN

0 A SGD S 10
14366

BAUHERR : SCHWEIZERISCHE BUNDESBAHNEN, BAUABTEILUNG KREIS II, SEKTION TIEFBAU, LUZERN

OBJEKT : AUSBAU BAHNHOF UND BAHNANLAGE TECKNAU

RAMMSONDIERUNG RS 9

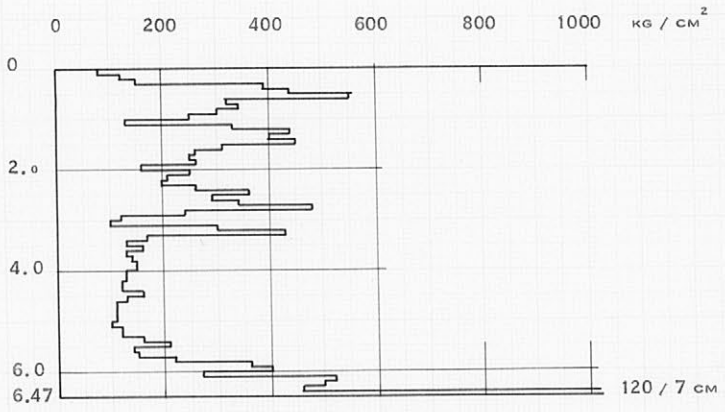

LUZERN, 23. 12. 1975
75 652 - 16 SP


BOHRUNTERNEHMUNG
GEBR. MENGIS LUZERN

0 A SGD S 10
14366

BAUHERR : SCHWEIZERISCHE BUNDESBAHNEN, BAUABTEILUNG KREIS II, SEKTION TIEFBAU, LUZERN

OBJEKT : AUSBAU BAHNHOF UND BAHNANLAGE TECKNAU

RAMMSONDIERUNG RS 10

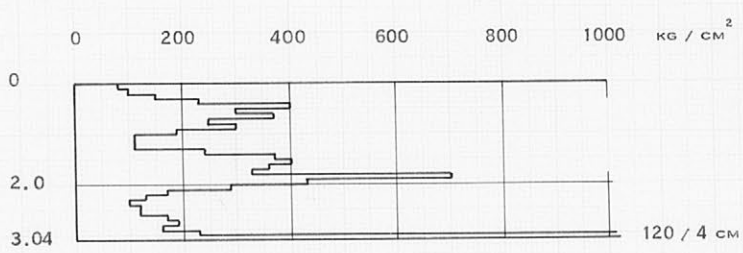

LUZERN, 23. 12. 1975
75 652 - 17 SP


BOHRUNTERNEHMUNG
GEBR. MENGIS LUZERN

0 A SGD S 10
14366

BAUHERR : SCHWEIZERISCHE BUNDESBAHNEN, BAUABTEILUNG KREIS II, SEKTION TIEFBAU, LUZERN

OBJEKT : AUSBAU BAHNHOF UND BAHNANLAGE TECKNAU

RAMMSONDIERUNG RS 11

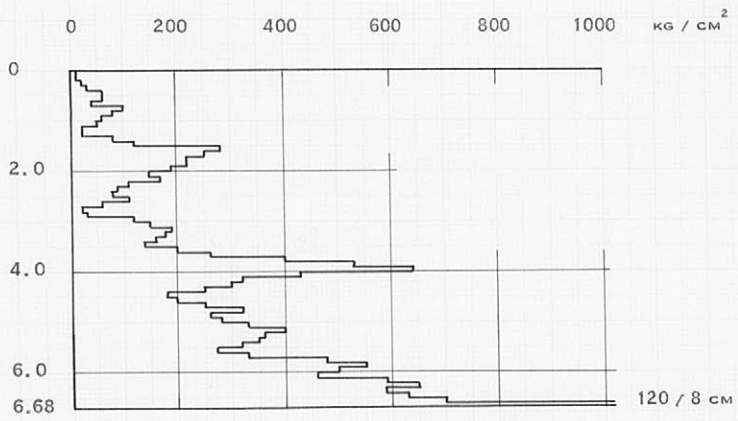

LUZERN, 23. 12. 1975
75 652 - 18 SP


BOHRUNTERNEHMUNG
GEBR. MENGIS LUZERN

0 A SGD S 10
14366

BAUHERR : SCHWEIZERISCHE BUNDESBAHNEN, BAUABTEILUNG KREIS II, SEKTION TIEFBAU, LUZERN

OBJEKT : AUSBAU BAHNHOF UND BAHNANLAGE TECKNAU

RAMMSONDIERUNG RS 12

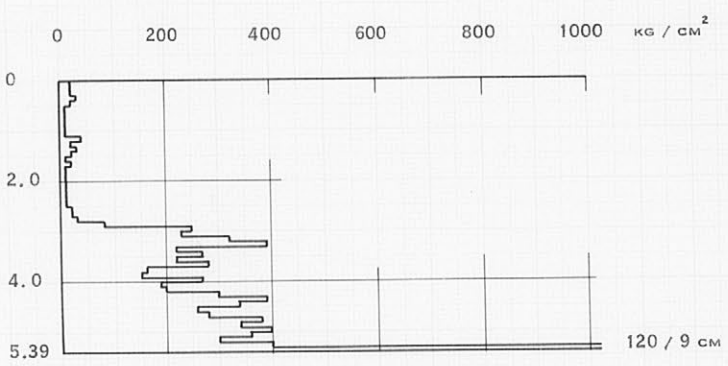

LUZERN, 23. 12. 1975
75 652 - 19 SP


BOHRUNTERNEHMUNG
GEBR. MENGIS LUZERN

0 A SGD S 10
14366

BAUHERR : SCHWEIZERISCHE BUNDESBAHNEN, BAUABTEILUNG KREIS II, SEKTION TIEFBAU, LUZERN

OBJEKT : AUSBAU BAHNHOF UND BAHNANLAGE TECKNAU

RAMMSONDIERUNG RS 13

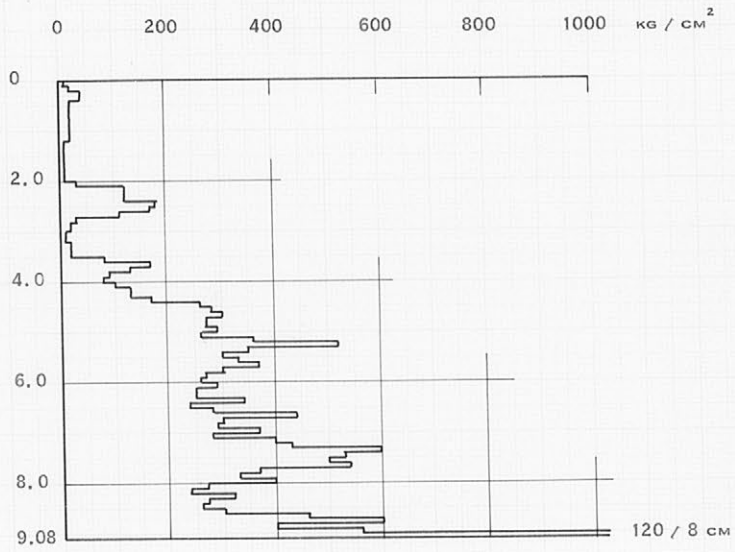

LUZERN, 23. 12. 1975
75 652 - 20 SP

BOHRUNTERNEHMUNG
GEBR. MENGIS LUZERN

0 A SGD S 10
14366